# Escalier demi-g-large

Escalier demi-tournant gauche · 17 hauteurs de 158,8 mm · giron 327,2 mm

## COTES

| | |
|---|---|
| Hauteur à monter | **2 700 mm** |
| Longueur côté départ | **2 600 mm** |
| Jour, limons compris | **400 mm** |
| Longueur côté arrivée | **2 600 mm** |
| Emmarchement | **850 mm** |
| Trémie | **2 650 mm × 2 190 mm** |
| Épaisseur du plancher | **200 mm** |
| Ligne de foulée (depuis le jour) | **425 mm** |
| Marches balancées | **5 et 5 · progressivité 60 %** |
| Premier tour | **marches 4 à 8 · 635 mm à 1 271 mm** |
| Second tour | **marches 9 à 13 · 1 429 mm à 2 065 mm** |

## CONTRÔLES


| | | |
|---|---|---|
| Hauteur de marche | **158,8 mm** | **Bon** |
| Giron | **327,2 mm** | **Limite** |
| Blondel 2h + g | **645 mm** | **Limite** |
| Pente | **25,9 °** | **Bon** |
| Échappée jour | **Libre** | **Bon** |
| Échappée foulée | **Libre** | **Bon** |
| Échappée mur | **Libre** | **Bon** |
| Giron mini au jour | **114 mm** | **Bon** |

## REMARQUES

- Giron long (327 mm) : ajoutez une hauteur pour un pas plus naturel.
- Loi de Blondel hors plage : 2h + g = 645 mm, visez 600 à 640 mm.
- Longueur côté départ conseillée : 2 480 mm, soit 17 hauteurs de 158,8 mm et un giron de 319,7 mm.
- Trémie minimale pour 2 000 mm d'échappée : 2 610 mm côté arrivée, avec 2 190 mm côté fond.
- Garde-corps : main courante de 900 à 1 071 mm au-dessus des nez, 4 montants et 29 lisses, écart libre de 103 mm au plus.
- La lisse basse touche le limon là où il monte plus vite que la main courante (tournant) : préférez des balustres.

**Rouvrir cet escalier**
sur quart-de-tour.fr

## PLAN

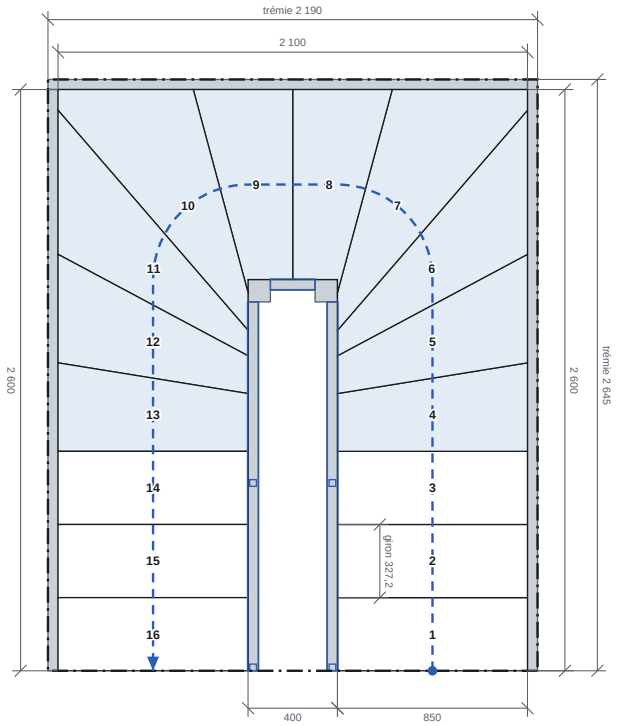

# Bois et fiche des marches

### BOIS

| | |
|---|---|
| Essence | **Chêne** |
| Épaisseur de marche | **40 mm** |
| Débord de nez | **30 mm** |
| Rayon du nez | **10,0 mm** |
| Contremarches | **22 mm** |

### LIMONS ET ASSEMBLAGE

| | |
|---|---|
| Épaisseur de limon | **45 mm** |
| Hauteur du limon de mur | **340 mm** |
| Hauteur du limon de jour | **550 mm** |
| Section du poteau | **100 mm** |
| Encastrement | **15 mm** |
| Jeu d'assemblage par côté | **0,5 mm** |
| Garde-corps | **Lisses rampantes dans le chant** |
| Main courante | **50 × 70 mm** |

### FICHE DES MARCHES

| MARCHE | DESSUS | GIRON JOUR | GIRON FOULÉE | GIRON EXTÉRIEUR | LONGUEUR DE NEZ |
|---|---|---|---|---|---|
| 1 | 158,8 | 327,2 | 327,2 | 327,2 | 850,0 |
| 2 | 317,6 | 327,2 | 327,2 | 327,2 | 850,0 |
| 3 | 476,5 | 327,2 | 327,2 | 327,2 | 850,0 |
| 4 | 635,3 | 258,5 | 327,2 | 395,9 | 850,0 |
| 5 | 794,1 | 168,9 | 327,2 | 485,5 | 861,0 |
| 6 | 952,9 | 113,6 | 327,2 | 644,5 | 963,6 |
| 7 | 1 111,8 | 168,9 | 327,2 | 697,5 | 1 301,0 |
| 8 | 1 270,6 | 258,5 | 327,2 | 445,0 | 941,0 |
| 9 | 1 429,4 | 258,5 | 327,2 | 445,0 | 850,0 |
| 10 | 1 588,2 | 168,9 | 327,2 | 697,5 | 941,0 |
| 11 | 1 747,1 | 113,6 | 327,2 | 644,5 | 1 301,0 |
| 12 | 1 905,9 | 168,9 | 327,2 | 485,5 | 963,6 |
| 13 | 2 064,7 | 258,5 | 327,2 | 395,9 | 861,0 |
| 14 | 2 223,5 | 327,2 | 327,2 | 327,2 | 850,0 |
| 15 | 2 382,4 | 327,2 | 327,2 | 327,2 | 850,0 |
| 16 | 2 541,2 | 327,2 | 327,2 | 327,2 | 850,0 |
| Palier | 2 700,0 | | | | |

marches balancées · cotes en millimètres

Girons mesurés de nez à nez. Repères de confort usuels (Blondel 600 à 640 mm, hauteur 160 à 185 mm, giron d'au moins 240 mm, échappée d'au moins 2 000 mm et jamais sous 1 900 mm) : à confronter au NF DTU 36.3 et aux exigences du chantier avant fabrication.

# Liste de débit

| PIÈCE | QTÉ | LONGUEUR | LARGEUR | ÉPAISSEUR |
|---|---|---|---|---|
| Limon de jour 1/3 | 1 | 2 096 | 627 | 45 |
| Limon de jour 2/3 | 1 | 280 | 673 | 45 |
| Limon de jour 3/3 | 1 | 2 274 | 627 | 45 |
| Limon de mur 1/3 | 1 | 2 882 | 458 | 45 |
| Limon de mur 2/3 | 1 | 2 299 | 444 | 45 |
| Limon de mur 3/3 | 1 | 2 903 | 457 | 45 |
| Marches 1, 2, 3, 14, 15, 16 | 6 | 880 | 380 | 40 |
| Marche 4 | 1 | 880 | 452 | 40 |
| Marche 5 | 1 | 980 | 543 | 40 |
| Marche 6 | 1 | 1 344 | 647 | 40 |
| Marche 7 | 1 | 1 416 | 566 | 40 |
| Marche 8 | 1 | 1 015 | 484 | 40 |
| Marche 9 | 1 | 1 179 | 503 | 40 |
| Marche 10 | 1 | 1 378 | 639 | 40 |
| Marche 11 | 1 | 1 471 | 466 | 40 |
| Marche 12 | 1 | 1 100 | 480 | 40 |
| Marche 13 | 1 | 941 | 445 | 40 |
| Contremarches 1, 2, 3, 4, 9, 14, 15, 16, 17 | 9 | 880 | 119 | 22 |
| Contremarches 5, 13 | 2 | 895 | 119 | 22 |
| Contremarches 6, 12 | 2 | 1 010 | 119 | 22 |
| Contremarches 7, 11 | 2 | 1 373 | 119 | 22 |
| Contremarche 8 | 1 | 918 | 119 | 22 |
| Contremarche 10 | 1 | 1 221 | 119 | 22 |
| Main courante 1/3 | 1 | 2 034 | 70 | 50 |
| Main courante 2/3 | 1 | 319 | 70 | 50 |
| Main courante 3/3 | 1 | 2 034 | 70 | 50 |
| Montant 1 | 1 | 809 | 30 | 30 |
| Montant 2 | 1 | 945 | 30 | 30 |
| Montant 3 | 1 | 840 | 30 | 30 |
| Montant 4 | 1 | 975 | 30 | 30 |
| Lisses 1, 2, 3, 4, 5, 6, 7, 8, 9, 10, 11, 12, 18, 19, 20, 21, 22, 23, 24, 25, 26, 27, 28, 29 | 24 | 968 | 30 | 30 |
| Lisses 13, 14, 15, 16, 17 | 5 | 254 | 30 | 30 |
| Poteau 1 | 1 | 2 330 | 100 | 100 |
| Poteau 2 | 1 | 2 760 | 100 | 100 |

Cotes brutes de débit en millimètres, longueur dans le fil.

**Volume brut débité : 0,759 m³ de chêne, soit environ 540 kg (710 kg/m³).**

### FABRICATION


- Tous les logements tiennent dans les limons, avec au moins 20 mm de bois dessous (limon de jour de 550 mm).
- Marches 6, 10 plus profondes que le plateau (jusqu'à 647 mm pour 600) : à reconstituer en lames collées, fil le long du nez.
- Limon de jour 1/3 (2 096 × 627 mm) plus grand que le plateau de 5 000 × 600 mm : à abouter ou à débiter dans un plateau plus grand.
- Limon de jour 2/3 (280 × 673 mm) plus grand que le plateau de 5 000 × 600 mm : à abouter ou à débiter dans un plateau plus grand.
- Limon de jour 3/3 (2 274 × 627 mm) plus grand que le plateau de 5 000 × 600 mm : à abouter ou à débiter dans un plateau plus grand.

# Limons

Escalier demi-g-large
Vus côté marches, couchés dans le sens du plateau · échelle 1:15


Cotes en millimètres : nez depuis le bout gauche du plateau, hauteurs depuis sa rive basse, angles depuis sa rive. Logements défoncés de 15 mm, jeu de 0,5 mm par côté.

## Limon de jour 1/3 2 096 × 627 × 45

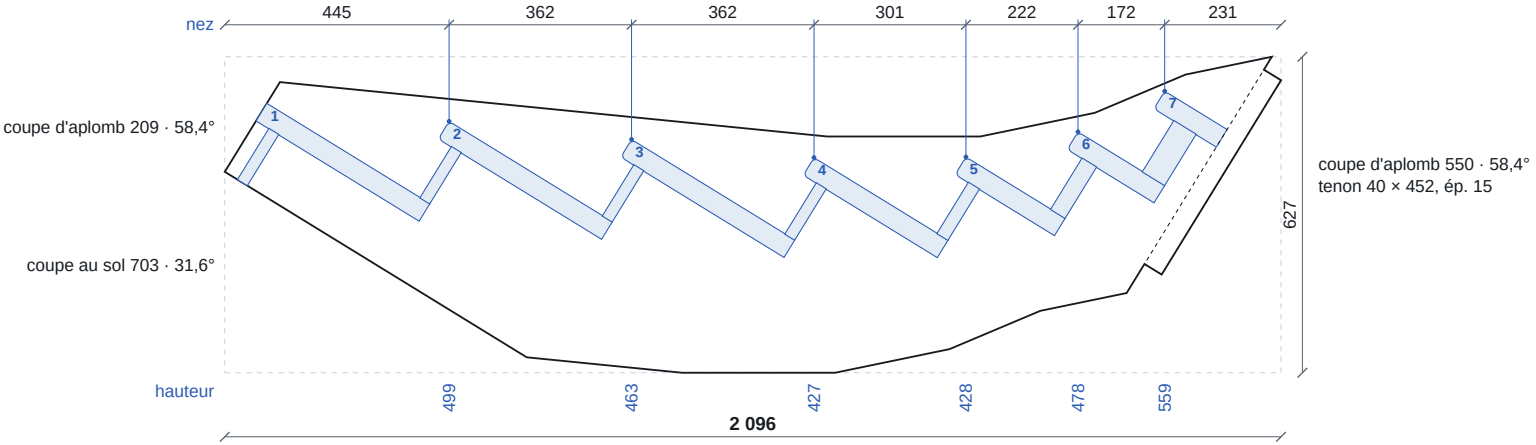


2 mortaises de balustres dans le chant haut.

## Limon de jour 2/3 280 × 673 × 45

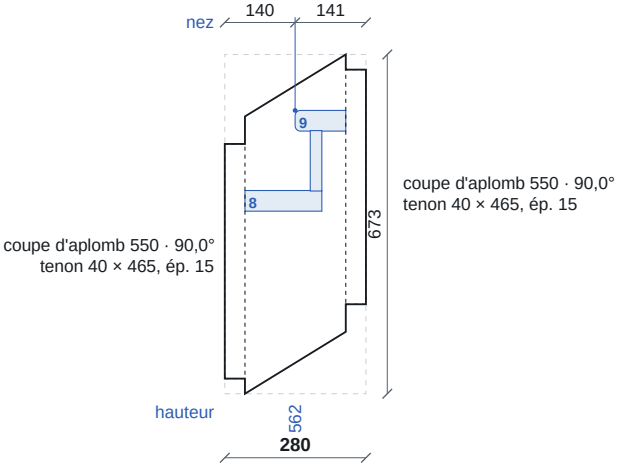


# Limons

Escalier demi-g-large
Vus côté marches, couchés dans le sens du plateau · échelle 1:15


Cotes en millimètres : nez depuis le bout gauche du plateau, hauteurs depuis sa rive basse, angles depuis sa rive. Logements défoncés de 15 mm, jeu de 0,5 mm par côté.

## Limon de jour 3/3 2 274 × 627 × 45

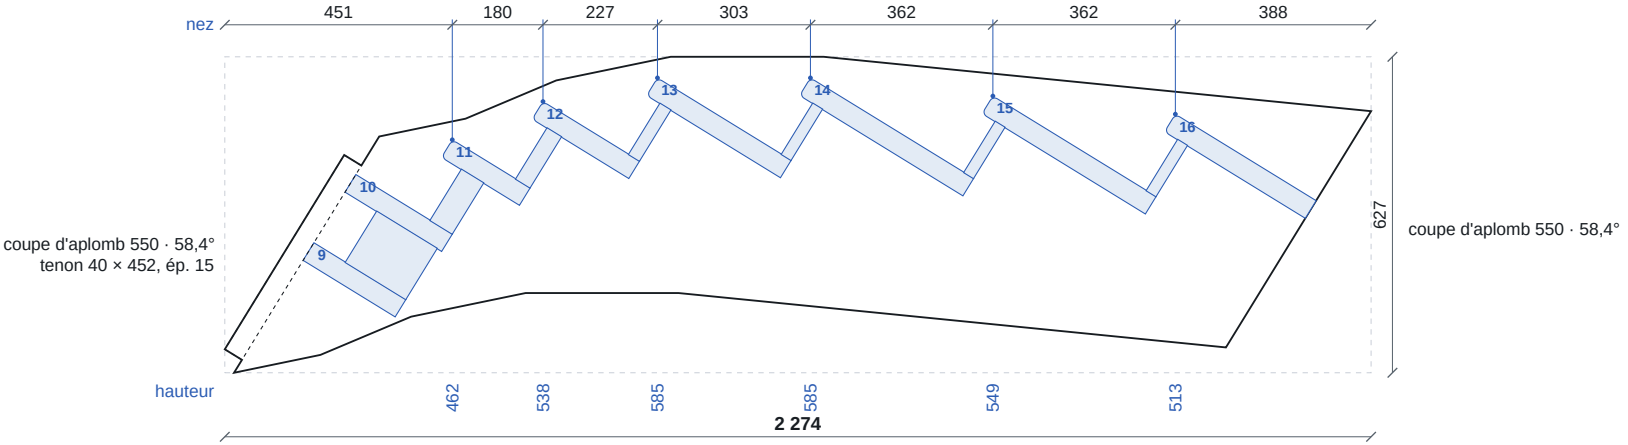


2 mortaises de balustres dans le chant haut.

## Limon de mur 1/3 2 882 × 458 × 45

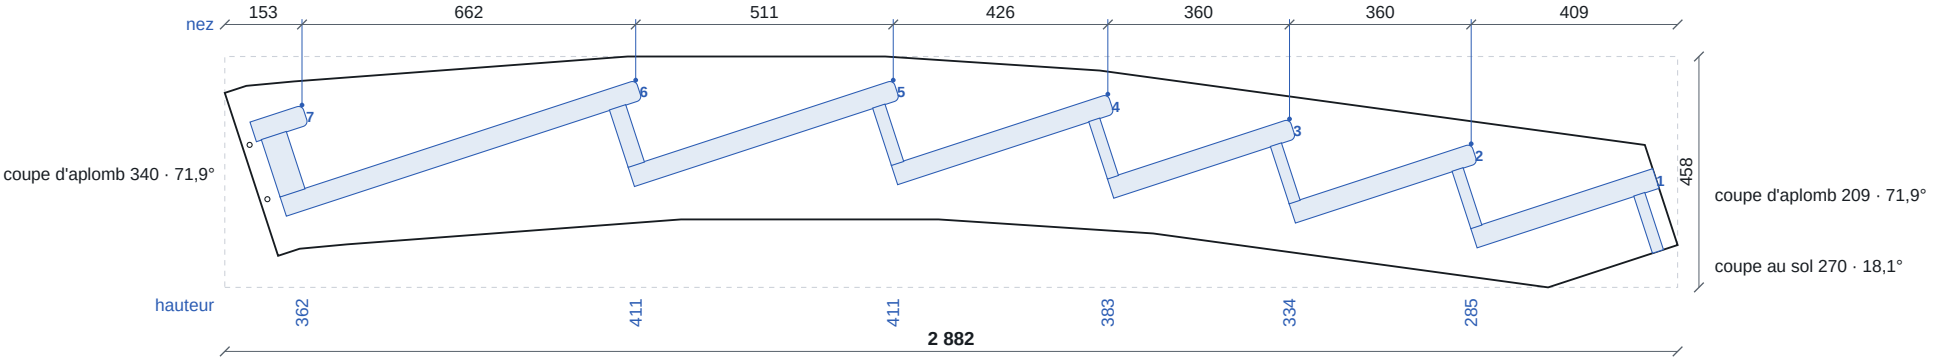



2 perçages Ø 10 traversants pour l'about du limon suivant : x 84, y 175 ; x 49, y 283.

# Limons



Cotes en millimètres : nez depuis le bout gauche du plateau, hauteurs depuis sa rive basse, angles depuis sa rive. Logements défoncés de 15 mm, jeu de 0,5 mm par côté.

## Limon de mur 2/3 2 299 × 444 × 45

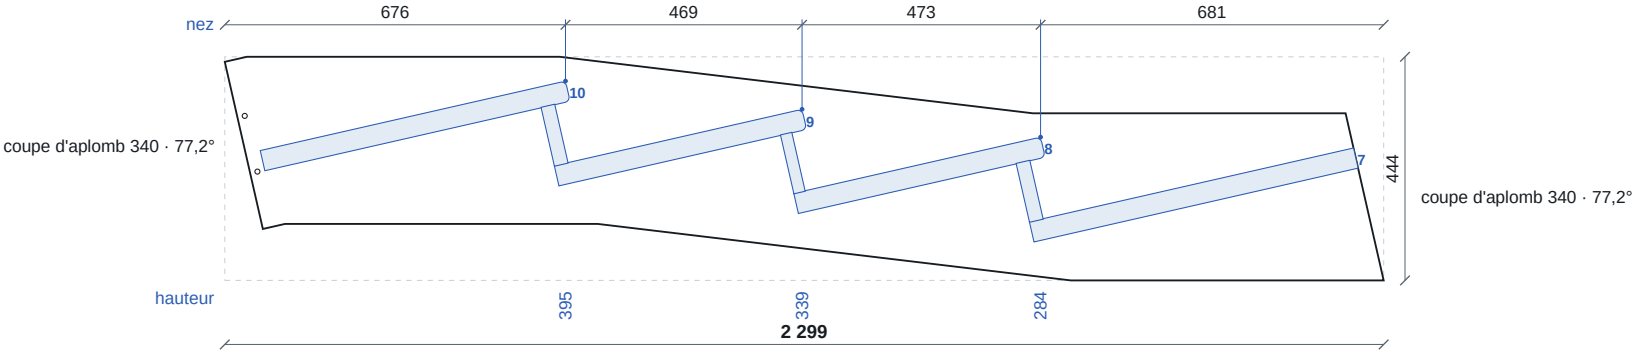


2 perçages Ø 10 traversants pour l'about du limon suivant : x 65, y 216 ; x 40, y 326.

## Limon de mur 3/3 2 903 × 457 × 45

