Escalier droit-debordantes-palier

Escalier droit · 15 hauteurs de 180,0 mm · giron 260,7 mm

COTES

Hauteur à monter	**2 700 mm**
Reculement	**3 650 mm**
Emmarchement	**850 mm**
Trémie	**3 200 mm**
Épaisseur du plancher	**200 mm**
Ligne de foulée (depuis le jour)	**425 mm**

CONTRÔLES


Hauteur de marche	**180,0 mm**	**Bon**
Giron	**260,7 mm**	**Bon**
Blondel 2h + g	**621 mm**	**Bon**
Pente	**34,6 °**	**Bon**
Échappée	**1 802 mm**	**Hors norme**
Reculement	**3 650 mm**	

REMARQUES

- Échappée de 1 802 mm sur toute la largeur, au-dessus de la marche 3 : pour 2 000 mm, allongez la trémie à 3 490 mm.
- Pas de garde-corps : côté vide, il en faut un dès 1 m de chute (main courante à 900 mm au moins, NF P01-012). Rien à faire si l'escalier est entre deux murs ou si le garde-corps est posé à part.

Rouvrir cet escalier
sur quart-de-tour.fr

PLAN

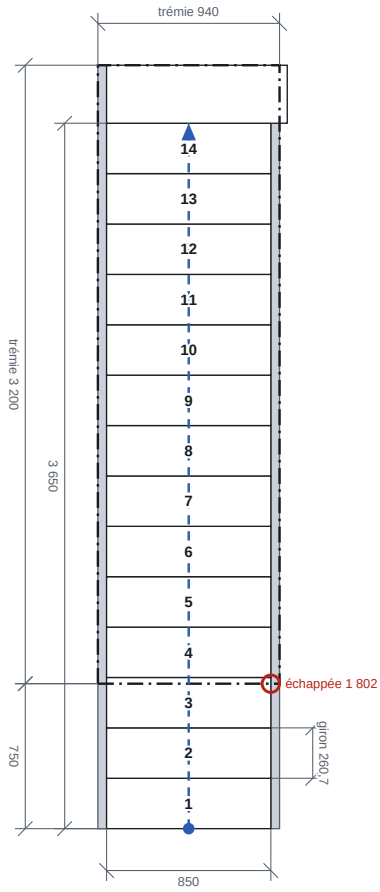

Bois et fiche des marches


BOIS

Essence	**Chêne**
Épaisseur de marche	**40 mm**
Débord de nez	**30 mm**
Profil du nez	**arrondi R10,0 dessus et dessous**
Rainures antidérapantes	**2 de 6 × 3 mm, entraxe 15**
Première rainure	**axe à 25 mm du nez**
Contremarches	**22 mm, derrière la marche**
Marches débordantes	**40 mm au jour**
Marche palière	**300 × 40 mm**


LIMONS ET ASSEMBLAGE

Épaisseur de limon	**45 mm**
Hauteur du limon gauche	**340 mm**
Limon droit, en crémaillère	**420 mm**
Encastrement	**15 mm**
Jeu d'assemblage par côté	**0,5 mm**
Garde-corps	**aucun**

VUE DE CÔTÉ, DÉVELOPPÉE SUR LA LIGNE DE FOULÉE

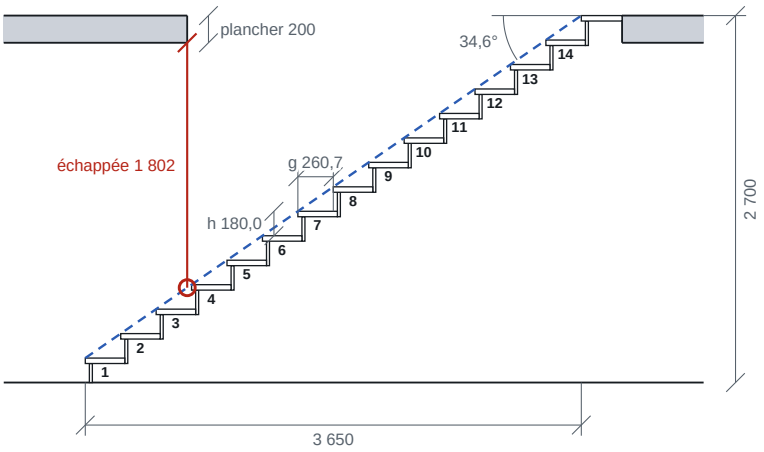

COUPE AU NEZ

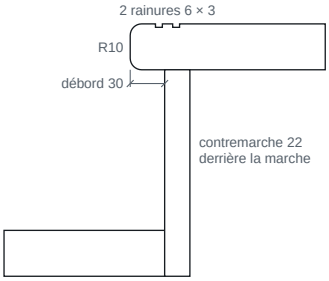

FICHE DES MARCHES

MARCHE	DESSUS	GIRON	LONGUEUR DE NEZ
1	180,0	260,7	850,0
2	360,0	260,7	850,0
3	540,0	260,7	850,0
4	720,0	260,7	850,0
5	900,0	260,7	850,0
6	1 080,0	260,7	850,0
7	1 260,0	260,7	850,0
8	1 440,0	260,7	850,0
9	1 620,0	260,7	850,0
10	1 800,0	260,7	850,0
11	1 980,0	260,7	850,0
12	2 160,0	260,7	850,0
13	2 340,0	260,7	850,0
14	2 520,0	260,7	850,0
Palier	2 700,0		

Cotes en millimètres.

Girons mesurés de nez à nez. Repères de confort usuels (Blondel 600 à 640 mm, hauteur 160 à 185 mm, giron d'au moins 240 mm, échappée d'au moins 2 000 mm et jamais sous 1 900 mm) : à confronter au NF DTU 36.3 et aux exigences du chantier avant fabrication.

Liste de débit

PIÈCE	QTÉ	LONGUEUR	LARGEUR	ÉPAISSEUR
Limon droit	1	4 720	413	45
Limon gauche	1	4 813	451	45
Marches 1, 2, 3, 4, 5, 6, 7, 8, 9, 10, 11, 12, 13, 14	14	950	291	40
Marche palière	1	950	300	40
Contremarche 1	1	910	140	22
Contremarches 2, 3, 4, 5, 6, 7, 8, 9, 10, 11, 12, 13, 14, 15	14	910	180	22

Cotes brutes de débit en millimètres, longueur dans le fil.

Volume brut débité : 0,404 m³ de chêne, soit environ 285 kg (710 kg/m³).

FABRICATION


- Tous les logements tiennent dans les limons, avec au moins 20 mm de bois dessous.
- Toutes les pièces tiennent dans un plateau de 5 000 × 600 mm.

Limons


Vus côté marches, couchés dans le sens du plateau · échelle 1:25

Cotes en millimètres : nez depuis le bout gauche du plateau, hauteurs depuis sa rive basse, angles depuis sa rive. Logements défoncés de 15 mm, jeu de 0,5 mm par côté. Points a, b, c… : voir le traçage à la main.

Limon droit 4 720 × 413 × 45

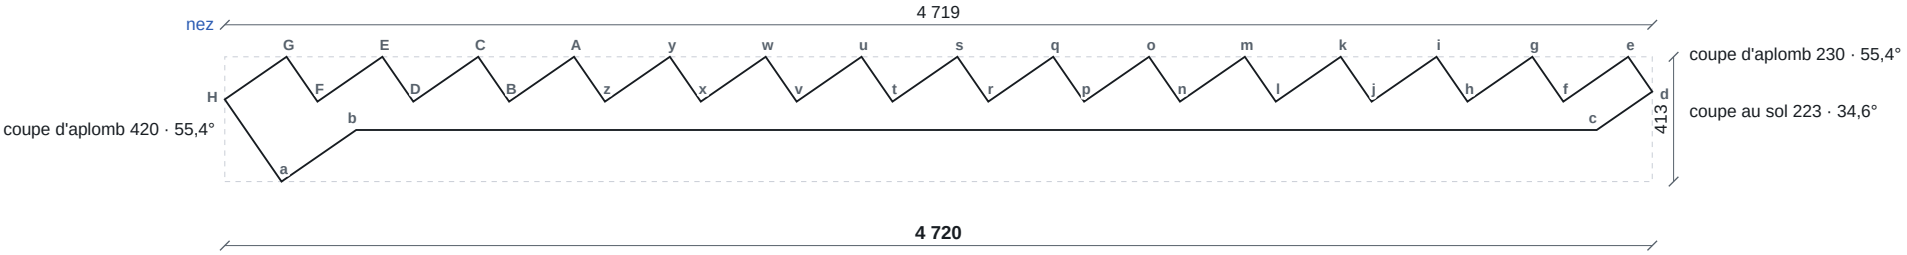

Limon gauche 4 813 × 451 × 45

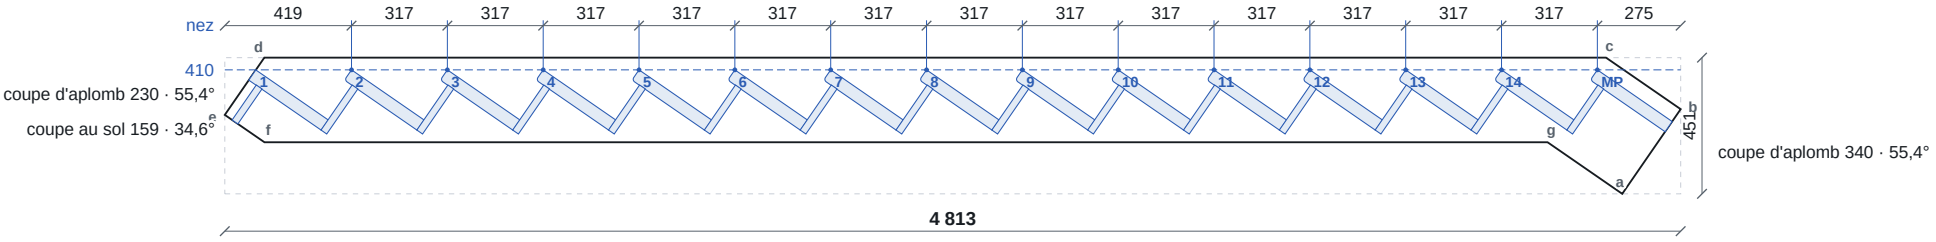

Traçage des limons

1. Dresser la rive basse du plateau et tracer le bout gauche d'équerre : x se mesure le long de la rive depuis ce bout, y d'équerre depuis la rive.
2. Contour : pointer a, b, c… et les joindre dans l'ordre. Les lettres sont aussi sur le dessin des limons.
3. Marches : pointer le nez et le fond, les joindre, c'est le dessus de la marche ; tracer le dessous parallèle, 41 mm plus bas (marche et jeu). Arrondir le bout côté nez au rayon 10.
4. Contremarches : sur le dessus de la marche, depuis le nez, pointer les deux distances données ; tracer d'équerre vers le bas jusqu'au dessus de la marche d'en dessous, ou jusqu'au sol.
5. Défoncer à 15 mm. Tous les dessus de marche d'un limon sont parallèles : la fausse équerre réglée comme indiqué les contrôle.

Limon droit

4 720 × 413 × 45 · dessus de marche à 34,6° sur la rive, montant vers la droite (fausse équerre : 1 000 le long de la rive, 690 d'équerre)

	Nez		Fond		Contremarche, depuis le nez	
Marche	x	y	x	y	de	à

Contour		
Point	x	y
a	187	0
b	434	170
c	4 535	170
d	4 719	297
e	4 639	412
f	4 425	264
g	4 323	412
h	4 108	264
i	4 006	412
j	3 791	264
k	3 689	412
l	3 475	264

Point	x	y
m	3 372	412
n	3 158	264
o	3 055	412
p	2 841	264
q	2 739	412
r	2 524	264
s	2 422	412
t	2 207	264
u	2 105	412
v	1 890	264
w	1 788	412
x	1 574	264

Point	x	y
y	1 471	412
z	1 257	264
A	1 155	412
B	940	264
C	838	412
D	623	264
E	521	412
F	306	264
G	204	412
H	0	272

Limon gauche

4 813 × 451 × 45 · dessus de marche à 34,6° sur la rive, descendant vers la droite (fausse équerre : 1 000 le long de la rive, 690 d'équerre)

	Nez		Fond		Contremarche, depuis le nez	
Marche	x	y	x	y	de	à
1 *	103	410	342	244	30	53
2	419	410	659	244	30	53
3	736	410	976	244	30	53
4	1 053	410	1 293	244	30	53
5	1 369	410	1 609	244	30	53
6	1 686	410	1 926	244	30	53
7	2 003	410	2 243	244	30	53
8	2 320	410	2 560	244	30	53
9	2 637	410	2 877	244	30	53
10	2 953	410	3 194	244	30	53
11	3 270	410	3 510	244	30	53
12	3 587	410	3 827	244	30	53
13	3 904	410	4 144	244	30	53
14	4 221	410	4 461	244	30	53
MP	4 538	410	4 785	239	–	–

* logement coupé par l'about : le point « nez » est pris sur l'about.

Contour		
Point	x	y
a	4 620	0
b	4 813	280
c	4 566	450

Point	x	y
d	131	450
e	0	261
f	131	170

Point	x	y
g	4 373	170