Escalier quart-d-manuel

Escalier quart tournant droit · 17 hauteurs de 158,8 mm · giron 224,8 mm

COTES

Hauteur à monter	**2 700 mm**
Longueur côté départ	**2 900 mm**
Longueur côté arrivée	**1 800 mm**
Emmarchement	**850 mm**
Trémie	**2 550 mm × 1 845 mm**
Épaisseur du plancher	**200 mm**
Ligne de foulée (depuis le jour)	**380 mm**
Marches balancées	**5 · progressivité 5 %**
Tour	**marches 9 à 13 · 1 429 mm à 2 065 mm**

CONTRÔLES


Hauteur de marche	**158,8 mm**	**Bon**
Giron	**224,8 mm**	**Limite**
Blondel 2h + g	**542 mm**	**Hors norme**
Pente	**35,2 °**	**Bon**
Échappée jour	**2 062 mm**	**Bon**
Échappée foulée	**2 062 mm**	**Bon**
Échappée mur	**2 062 mm**	**Bon**
Giron mini au jour	**100 mm**	**Limite**

REMARQUES

- Giron court (225 mm) sur la ligne de foulée : il manque de la longueur au sol.
- Loi de Blondel hors plage : 2h + g = 542 mm, visez 600 à 640 mm.
- Le calcul automatique (15 hauteurs) rend l'escalier confortable sans changer les longueurs.
- Giron côté jour de 100 mm seulement : augmentez le nombre de marches balancées (6 suffisent).
- Progressivité limitée à 5 % pour garder au moins 100 mm au jour.
- Trémie minimale pour 2 000 mm d'échappée : 2 470 mm côté départ, avec 1 845 mm côté arrivée.

Rouvrir cet escalier
sur quart-de-tour.fr

PLAN

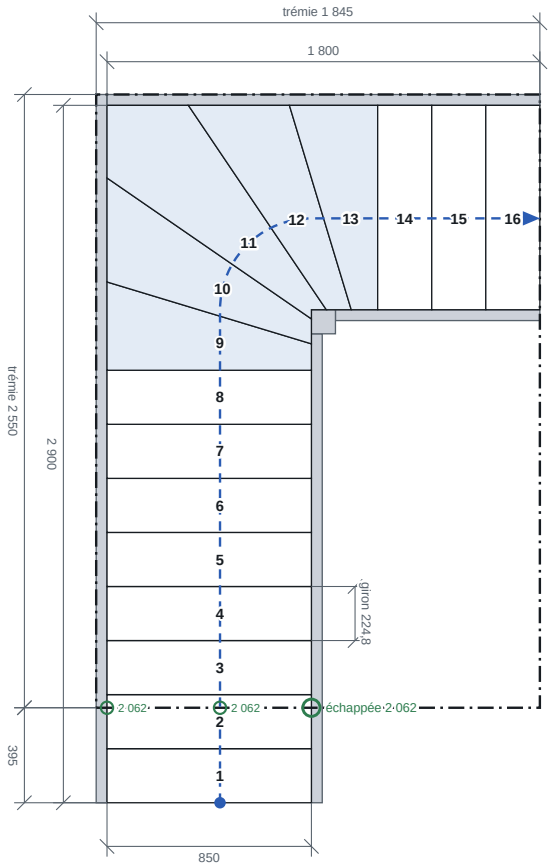

Bois et fiche des marches

BOIS

Essence	**Chêne**
Épaisseur de marche	**40 mm**
Débord de nez	**30 mm**
Rayon du nez	**10,0 mm**
Contremarches	**sans**

LIMONS ET ASSEMBLAGE

Épaisseur de limon	**45 mm**
Hauteur du limon de mur	**340 mm**
Hauteur du limon de jour	**330 mm**
Section du poteau	**100 mm**
Encastrement	**15 mm**
Jeu d'assemblage par côté	**0,5 mm**
Garde-corps	**aucun**

FICHE DES MARCHES

MARCHE	DESSUS	GIRON JOUR	GIRON FOULÉE	GIRON EXTÉRIEUR	LONGUEUR DE NEZ
1	158,8	224,8	224,8	224,8	850,0
2	317,6	224,8	224,8	224,8	850,0
3	476,5	224,8	224,8	224,8	850,0
4	635,3	224,8	224,8	224,8	850,0
5	794,1	224,8	224,8	224,8	850,0
6	952,9	224,8	224,8	224,8	850,0
7	1 111,8	224,8	224,8	224,8	850,0
8	1 270,6	224,8	224,8	224,8	850,0
9	1 429,4	109,8	224,8	367,0	850,0
10	1 588,2	103,7	224,8	432,6	888,1
11	1 747,1	100,0	224,8	640,3	1 032,4
12	1 905,9	103,7	224,8	420,2	1 025,5
13	2 064,7	109,8	224,8	367,0	888,1
14	2 223,5	224,8	224,8	224,8	850,0
15	2 382,4	224,8	224,8	224,8	850,0
16	2 541,2	224,8	224,8	224,8	850,0
Palier	2 700,0				

marches balancées · cotes en millimètres

Girons mesurés de nez à nez. Repères de confort usuels (Blondel 600 à 640 mm, hauteur 160 à 185 mm, giron d'au moins 240 mm, échappée d'au moins 2 000 mm et jamais sous 1 900 mm) : à confronter au NF DTU 36.3 et aux exigences du chantier avant fabrication.

Liste de débit

PIÈCE	QTÉ	LONGUEUR	LARGEUR	ÉPAISSEUR
Limon de jour 1/2	1	2 591	364	45
Limon de jour 2/2	1	1 325	381	45
Limon de mur 1/2	1	3 486	619	45
Limon de mur 2/2	1	2 136	482	45
Marches 1, 2, 3, 4, 5, 6, 7, 8, 14, 15, 16	11	880	255	40
Marche 9	1	880	403	40
Marche 10	1	1 057	455	40
Marche 11	1	1 301	468	40
Marche 12	1	1 135	379	40
Marche 13	1	959	385	40
Poteau	1	2 120	100	100

Cotes brutes de débit en millimètres, longueur dans le fil.

Volume brut débité : 0,418 m³ de chêne, soit environ 295 kg (710 kg/m³).

FABRICATION


- Tous les logements tiennent dans les limons, avec au moins 20 mm de bois dessous (limon de jour de 330 mm).
- Limon de mur 1/2 (3 486 × 619 mm) plus grand que le plateau de 5 000 × 600 mm : à abouter ou à débiter dans un plateau plus grand.

Limons


Vus côté marches, couchés dans le sens du plateau · échelle 1:20

Cotes en millimètres : nez depuis le bout gauche du plateau, hauteurs depuis sa rive basse, angles depuis sa rive. Logements défoncés de 15 mm, jeu de 0,5 mm par côté.


Limon de jour 1/2 2 591 × 364 × 45

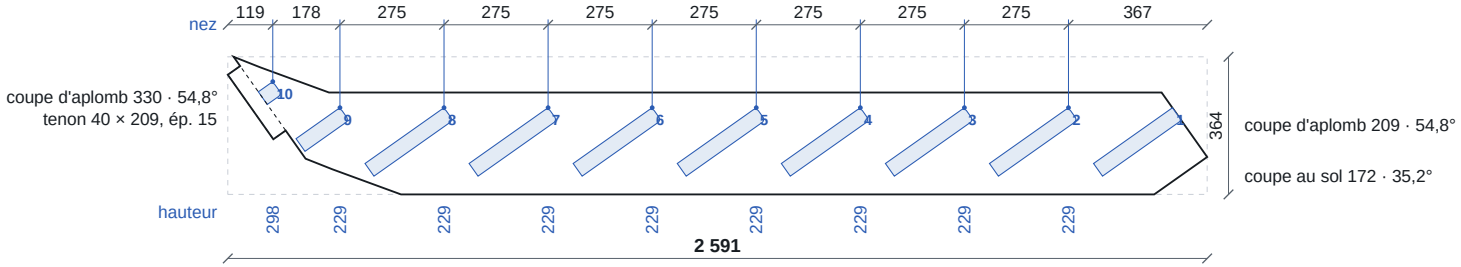

Limon de jour 2/2 1 325 × 381 × 45

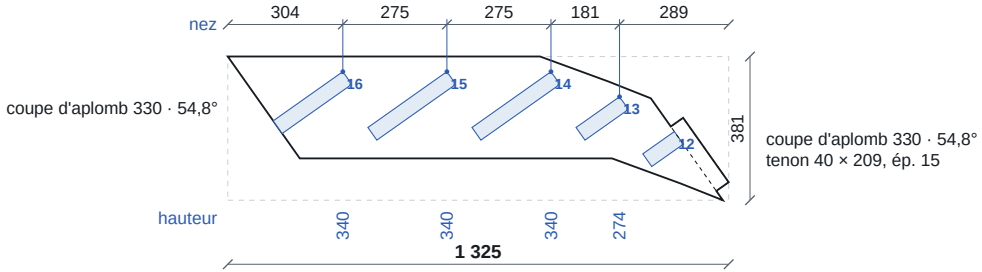

Limon de mur 1/2 3 486 × 619 × 45

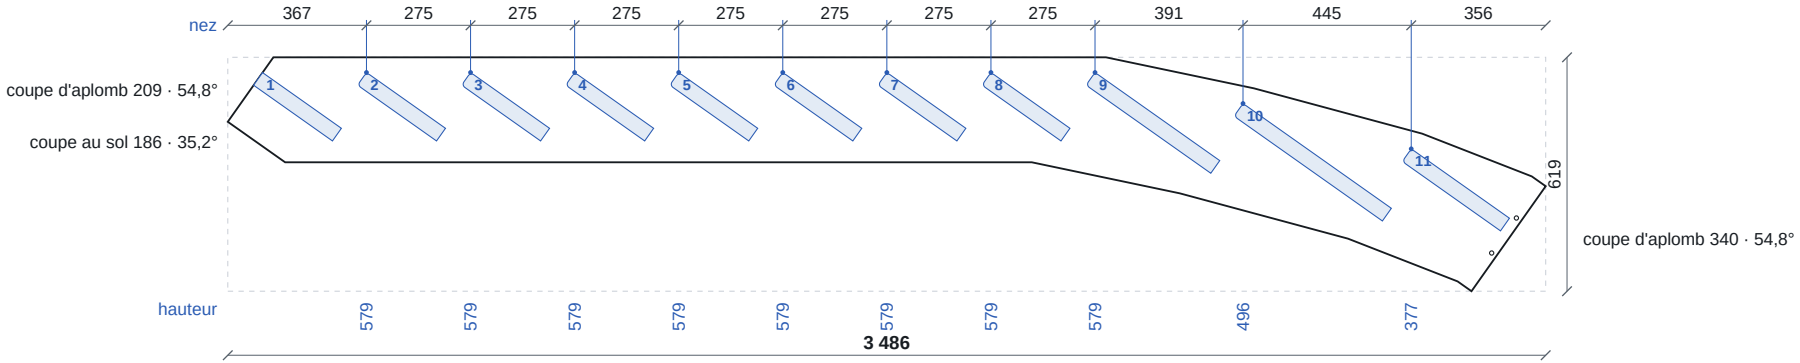

2 perçages Ø 10 traversants pour l'about du limon suivant : x 3 343, y 101 ; x 3 408, y 194.

Limons

Cotes en millimètres : nez depuis le bout gauche du plateau, hauteurs depuis sa rive basse, angles depuis sa rive. Logements défoncés de 15 mm, jeu de 0,5 mm par côté.

Limon de mur 2/2 2 136 × 482 × 45

