Escalier dq-g-a-palier-mp-u

Escalier double quart tournant gauche · 15 hauteurs de 180,0 mm · giron 250,0 mm

COTES

Hauteur à monter	**2 700 mm**
Longueur côté départ	**1 950 mm**
Longueur côté fond	**2 550 mm**
Longueur côté arrivée	**2 100 mm**
Emmarchement	**850 mm**
Trémie prévue	**2 410 mm × 2 640 mm, en U (branches 1 000 et 1 000)**
Épaisseur du plancher	**200 mm**
Ligne de foulée (depuis le jour)	**425 mm**
Palier 1	**marche 5 · 950 mm de profondeur**
Palier 2	**marche 9 · 950 mm de profondeur**

CONTRÔLES


Hauteur de marche	**180,0 mm**	**Bon**
Giron	**250,0 mm**	**Bon**
Blondel 2h + g	**610 mm**	**Bon**
Pente	**35,8 °**	**Bon**
Échappée jour	**Libre**	**Bon**
Échappée foulée	**Libre**	**Bon**
Échappée mur	**Libre**	**Bon**
Paliers	**950 et 950 mm**	

REMARQUES

- Escalier confortable : tout est dans les règles.
- Palier 1 de 950 mm de profondeur : le reste de la division des girons s'y ajoute. Longueur côté départ de 1 918 mm pour le palier le plus court.
- Palier 2 de 950 mm de profondeur : le reste de la division des girons s'y ajoute. Longueur côté fond de 2 518 mm pour le palier le plus court.
- Trémie en U à prévoir pour 2 000 mm d'échappée : 2 410 mm côté arrivée, sur toute la largeur (2 640 mm), branches de 1 000 mm.
- Garde-corps : main courante de 900 à 900 mm au-dessus des nez, 24 balustres, écart libre de 115 mm au plus.

Rouvrir cet escalier
sur quart-de-tour.fr

PLAN

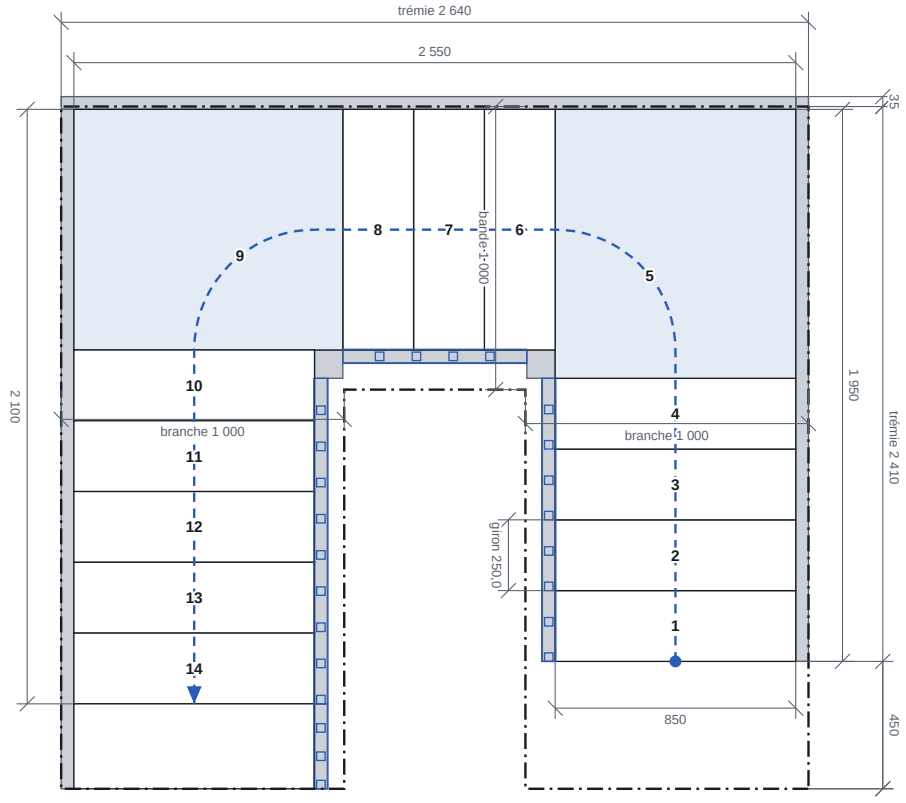

Bois et fiche des marches


BOIS

Essence	**Chêne**
Épaisseur de marche	**40 mm**
Débord de nez	**30 mm**
Rayon du nez	**10,0 mm**
Contremarches	**22 mm**
Marche palière	**300 × 40 mm**

LIMONS ET ASSEMBLAGE

Épaisseur de limon	**45 mm**
Hauteur du limon de mur	**340 mm**
Hauteur du limon de jour	**330 mm**
Section du poteau	**100 mm**
Encastrement	**15 mm**
Jeu d'assemblage par côté	**0,5 mm**
Garde-corps	**Balustres dans le chant**
Main courante	**50 × 70 mm**

VUE DE CÔTÉ, DÉVELOPPÉE SUR LA LIGNE DE FOULÉE

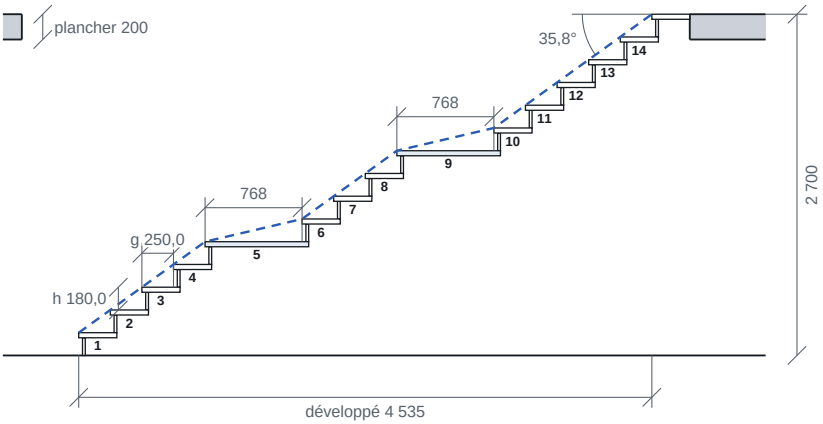

Échappée libre : tout l'escalier passe sous la trémie.

FICHE DES MARCHES

MARCHE	DESSUS	GIRON JOUR	GIRON FOULÉE	GIRON EXTÉRIEUR	LONGUEUR DE NEZ
1	180,0	250,0	250,0	250,0	850,0
2	360,0	250,0	250,0	250,0	850,0
3	540,0	250,0	250,0	250,0	850,0
4	720,0	250,0	250,0	250,0	850,0
5 palier	900,0	100,0	767,6	1 800,0	850,0
6	1 080,0	250,0	250,0	250,0	850,0
7	1 260,0	250,0	250,0	250,0	850,0
8	1 440,0	250,0	250,0	250,0	850,0
9 palier	1 620,0	100,0	767,6	1 800,0	850,0
10	1 800,0	250,0	250,0	250,0	850,0
11	1 980,0	250,0	250,0	250,0	850,0
12	2 160,0	250,0	250,0	250,0	850,0
13	2 340,0	250,0	250,0	250,0	850,0
14	2 520,0	250,0	250,0	250,0	850,0
Palier	2 700,0				

marches balancées · cotes en millimètres

Girons mesurés de nez à nez. Repères de confort usuels (Blondel 600 à 640 mm, hauteur 160 à 185 mm, giron d'au moins 240 mm, échappée d'au moins 2 000 mm et jamais sous 1 900 mm) : à confronter au NF DTU 36.3 et aux exigences du chantier avant fabrication.

Liste de débit

PIÈCE	QTÉ	LONGUEUR	LARGEUR	ÉPAISSEUR
Limon de jour 1/3	1	1 382	268	45
Limon de jour 2/3	1	1 024	268	45
Limon de jour 3/3	1	1 869	444	45
Limon de mur 1/3	1	2 175	858	45
Limon de mur 2/3	1	2 595	1 060	45
Limon de mur 3/3	1	2 778	802	45
Marches 1, 2, 3, 4, 6, 8, 10, 11, 12, 13, 14	11	880	302	40
Marche 7	1	880	303	40
Palier 1	1	917	965	40
Palier 2	1	917	965	40
Marche palière	1	880	300	40
Contremarches 1, 2, 3, 4, 5, 6, 7, 8, 9, 10, 11, 12, 13, 14, 15	15	880	140	22
Main courante 1/3	1	1 302	70	50
Main courante 2/3	1	889	70	50
Main courante 3/3	1	1 486	70	50
Retour de main courante	1	300	70	50
Balustres 1, 2, 3, 4, 5, 6, 7, 8, 9, 10, 11, 12, 13, 14, 15, 16, 17, 18, 19, 20, 21	21	804	30	30
Balustres 22, 23, 24	3	820	30	30
Poteau 1	1	2 120	100	100
Poteau 2	1	2 840	100	100

Cotes brutes de débit en millimètres, longueur dans le fil.

Volume brut débité : 0,705 m³ de chêne, soit environ 500 kg (710 kg/m³).


FABRICATION

- Tous les logements tiennent dans les limons, avec au moins 20 mm de bois dessous (limon de jour de 330 mm).
- Paliers de 917 × 965 et 917 × 965 mm : plateau collé à chant, fil le long du nez, logé comme une marche.
- Limon de mur 1/3 (2 175 × 858 mm) plus grand que le plateau de 5 000 × 600 mm : à abouter ou à débiter dans un plateau plus grand.
- Limon de mur 2/3 (2 595 × 1 060 mm) plus grand que le plateau de 5 000 × 600 mm : à abouter ou à débiter dans un plateau plus grand.
- Limon de mur 3/3 (2 778 × 802 mm) plus grand que le plateau de 5 000 × 600 mm : à abouter ou à débiter dans un plateau plus grand.

Limons


Cotes en millimètres : nez depuis le bout gauche du plateau, hauteurs depuis sa rive basse, angles depuis sa rive. Logements défoncés de 15 mm, jeu de 0,5 mm par côté.

Limon de jour 1/3 1 382 × 268 × 45

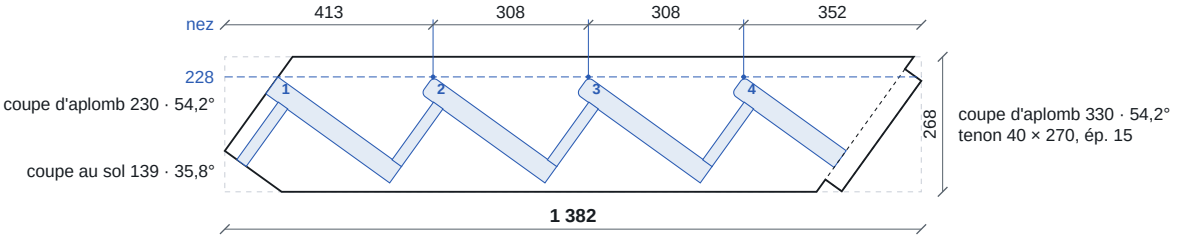


8 mortaises de balustres dans le chant haut.

Limon de jour 2/3 1 024 × 268 × 45

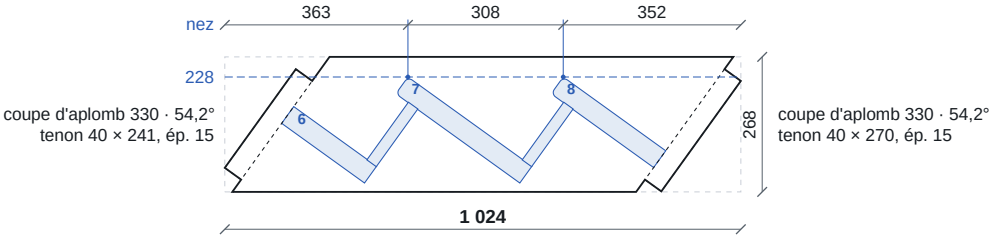

4 mortaises de balustres dans le chant haut.

Limon de jour 3/3 1 869 × 444 × 45

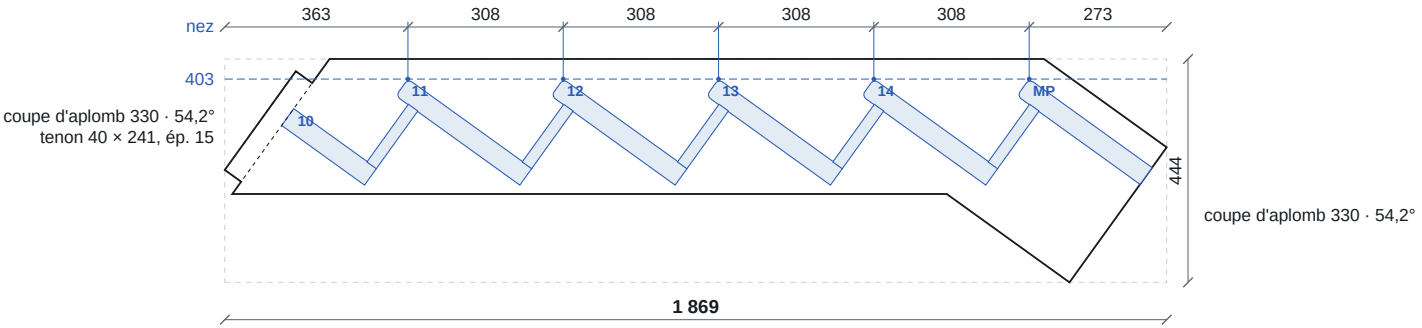


12 mortaises de balustres dans le chant haut.

Limons

Cotes en millimètres : nez depuis le bout gauche du plateau, hauteurs depuis sa rive basse, angles depuis sa rive. Logements défoncés de 15 mm, jeu de 0,5 mm par côté.

Limon de mur 1/3 2 175 × 858 × 45

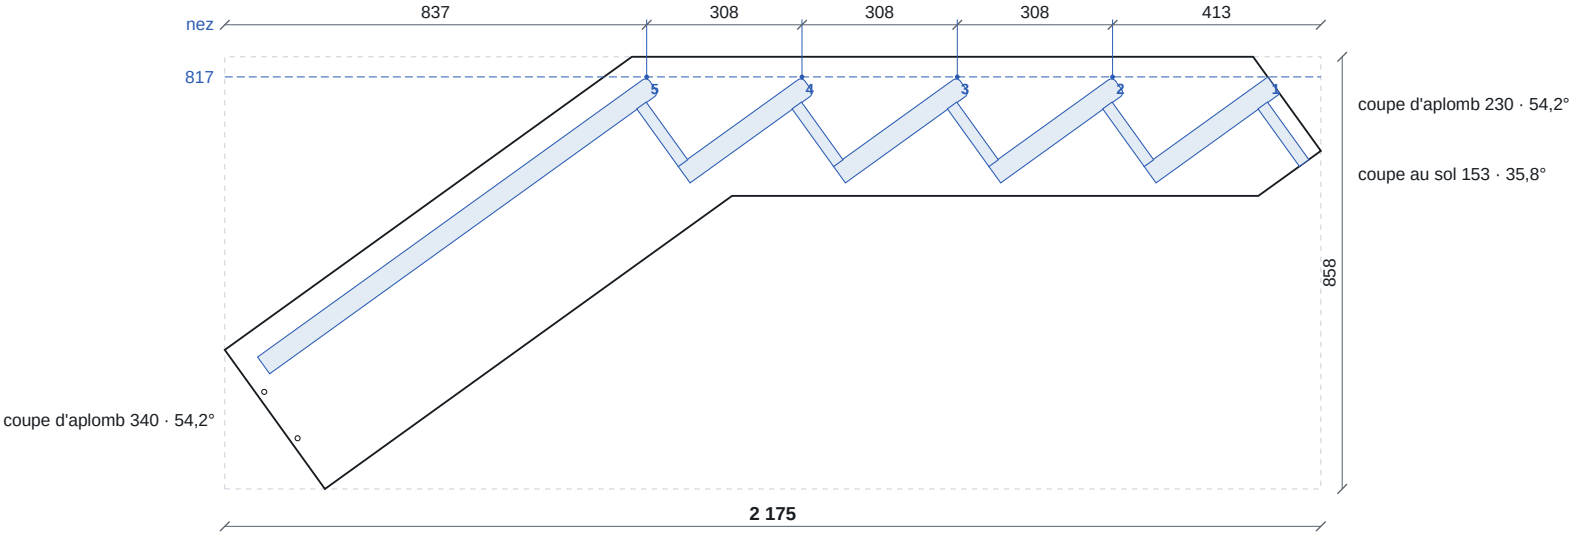


2 perçages Ø 10 traversants pour l'about du limon suivant : x 144, y 101 ; x 78, y 193.

Limons

Cotes en millimètres : nez depuis le bout gauche du plateau, hauteurs depuis sa rive basse, angles depuis sa rive. Logements défoncés de 15 mm, jeu de 0,5 mm par côté.

Limon de mur 2/3 2 595 × 1 060 × 45

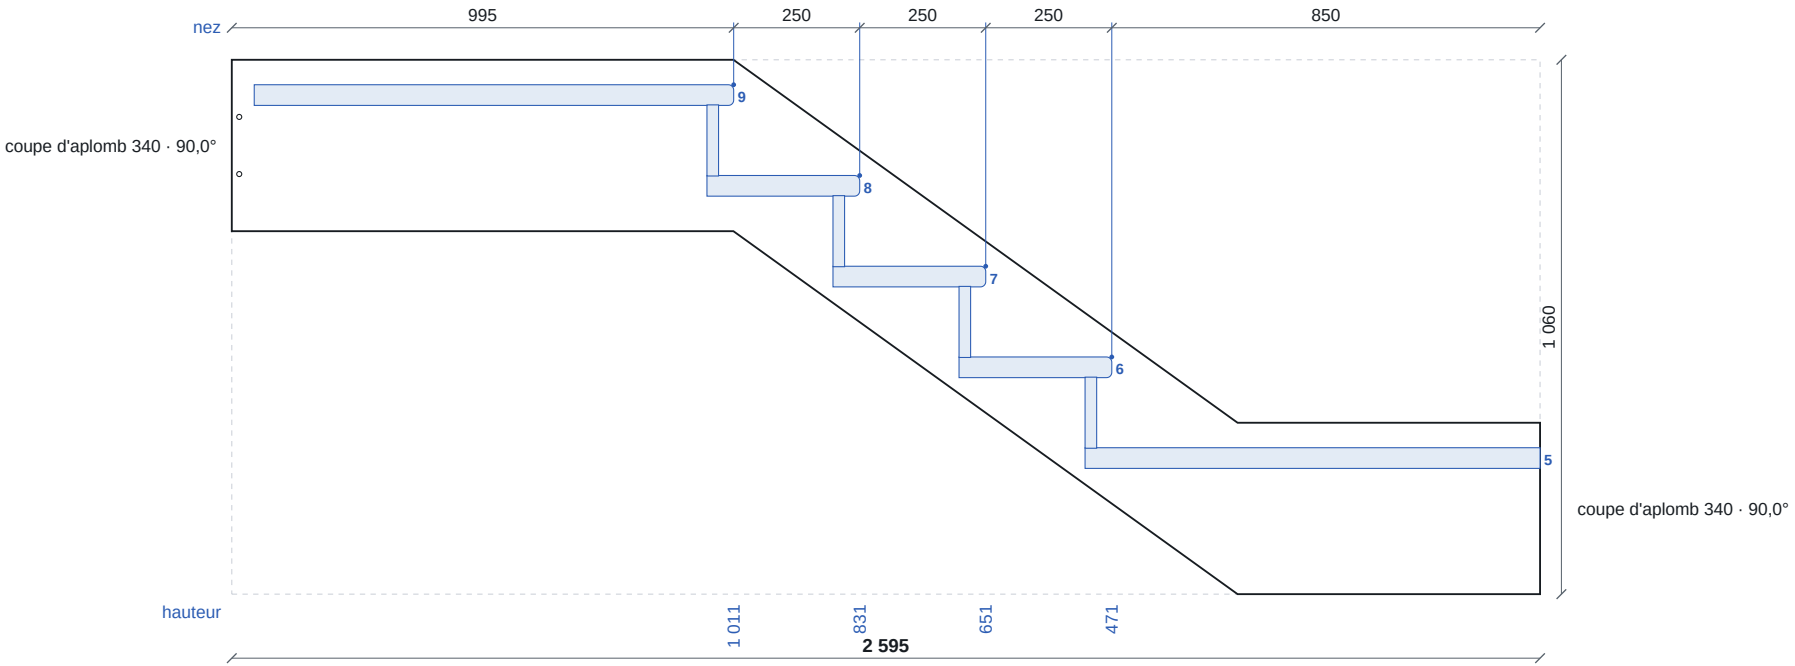

2 perçages Ø 10 traversants pour l'about du limon suivant : x 15, y 833 ; x 15, y 947.

Limons

Vus côté marches, couchés dans le sens du plateau · échelle 1:15

Cotes en millimètres : nez depuis le bout gauche du plateau, hauteurs depuis sa rive basse, angles depuis sa rive. Logements défoncés de 15 mm, jeu de 0,5 mm par côté.

Limon de mur 3/3 2 778 × 802 × 45

