Escalier demi-g

Escalier demi-tournant gauche · 17 hauteurs de 158,8 mm · giron 314,7 mm

COTES

Hauteur à monter	**2 700 mm**
Longueur côté départ	**2 600 mm**
Jour, limons compris	**200 mm**
Longueur côté arrivée	**2 600 mm**
Emmarchement	**850 mm**
Trémie	**2 650 mm × 1 990 mm**
Épaisseur du plancher	**200 mm**
Ligne de foulée (depuis le jour)	**425 mm**
Marches balancées	**5 et 5 · progressivité 60 %**
Premier tour	**marches 4 à 8 · 635 mm à 1 271 mm**
Second tour	**marches 9 à 13 · 1 429 mm à 2 065 mm**

CONTRÔLES


Hauteur de marche	**158,8 mm**	Bon
Giron	**314,7 mm**	Bon
Blondel 2h + g	**632 mm**	Bon
Pente	**26,8 °**	Bon
Échappée jour	**Libre**	Bon
Échappée foulée	**Libre**	Bon
Échappée mur	**Libre**	Bon
Giron mini au jour	**101 mm**	Bon

REMARQUES

- Escalier confortable : tout est dans les règles.
- Giron côté jour de 101 mm : au-dessus des 100 mm, mais beaucoup visent 120 à 150 mm au collet ; 9 marches balancées donnent 120 mm au moins.
- Trémie minimale pour 2 000 mm d'échappée : 2 610 mm côté arrivée, avec 1 990 mm côté fond.
- Pas de garde-corps : côté vide, il en faut un dès 1 m de chute (main courante à 900 mm au moins, NF P01-012). Rien à faire si l'escalier est entre deux murs ou si le garde-corps est posé à part.

Rouvrir cet escalier
sur quart-de-tour.fr

PLAN

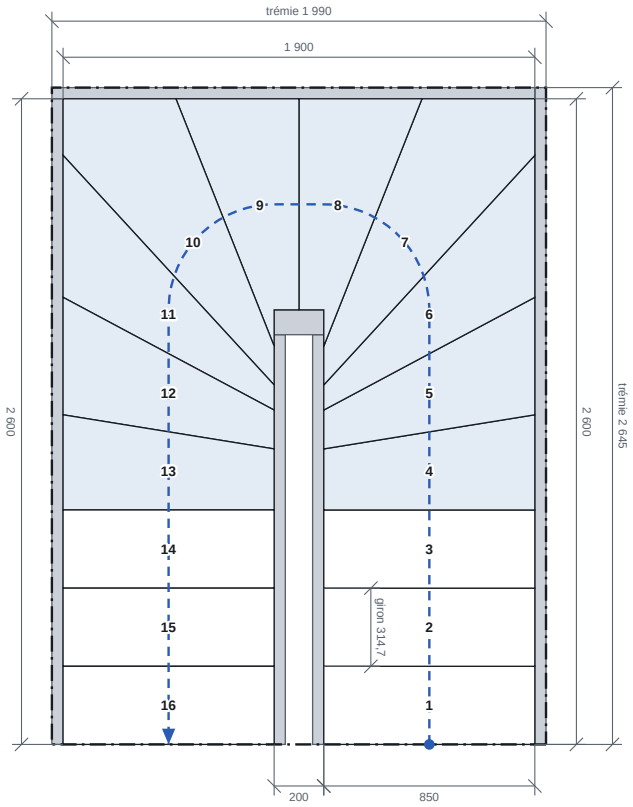

Bois et fiche des marches


BOIS

Essence	**Chêne**
Épaisseur de marche	**40 mm**
Débord de nez	**30 mm**
Profil du nez	**arrondi R10,0 dessus et dessous**
Contremarches	**22 mm, sur la marche**

LIMONS ET ASSEMBLAGE


Épaisseur de limon	**45 mm**
Hauteur du limon de mur	**340 mm**
Hauteur du limon de jour	**470 mm**
Section du poteau	**100 mm**
Encastrement	**15 mm**
Jeu d'assemblage par côté	**0,5 mm**
Garde-corps	**aucun**

VUE DE CÔTÉ, DÉVELOPPÉE SUR LA LIGNE DE FOULÉE

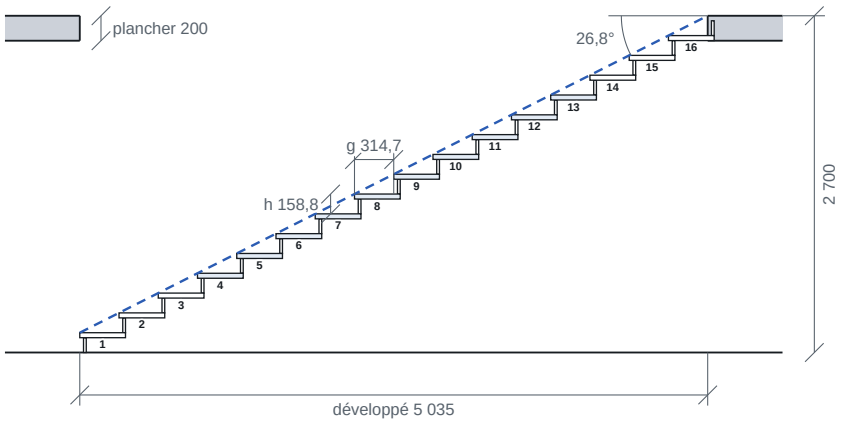

Échappée libre : tout l'escalier passe sous la trémie.

COUPE AU NEZ

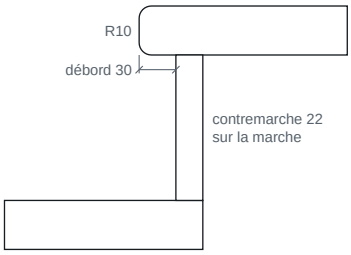

FICHE DES MARCHES

MARCHE	DESSUS	GIRON JOUR	GIRON FOULÉE	GIRON EXTÉRIEUR	LONGUEUR DE NEZ
1	158,8	314,7	314,7	314,7	850,0
2	317,6	314,7	314,7	314,7	850,0
3	476,5	314,7	314,7	314,7	850,0
4	635,3	246,0	314,7	383,4	850,0
5	794,1	156,4	314,7	473,0	861,0
6	952,9	101,1	314,7	571,9	963,6
7	1 111,8	156,4	314,7	682,0	1 256,1
8	1 270,6	246,0	314,7	495,6	1 071,7
9	1 429,4	246,0	314,7	495,6	850,0
10	1 588,2	156,4	314,7	682,0	1 071,7
11	1 747,1	101,1	314,7	571,9	1 256,1
12	1 905,9	156,4	314,7	473,0	963,6
13	2 064,7	246,0	314,7	383,4	861,0
14	2 223,5	314,7	314,7	314,7	850,0
15	2 382,4	314,7	314,7	314,7	850,0
16	2 541,2	314,7	314,7	314,7	850,0
Palier	2 700,0				

marches balancées · cotes en millimètres

Girons mesurés de nez à nez. Repères de confort usuels (Blondel 600 à 640 mm, hauteur 160 à 185 mm, giron d'au moins 240 mm, échappée d'au moins 2 000 mm et jamais sous 1 900 mm) : à confronter au NF DTU 36.3 et aux exigences du chantier avant fabrication.

Liste de débit

PIÈCE	QTÉ	LONGUEUR	LARGEUR	ÉPAISSEUR
Limon de jour 1/2	1	2 136	571	45
Limon de jour 2/2	1	2 278	571	45
Limon de mur 1/3	1	2 895	461	45
Limon de mur 2/3	1	2 092	416	45
Limon de mur 3/3	1	2 918	459	45
Marches 1, 2, 3, 14, 15, 16	6	880	367	40
Marche 4	1	880	439	40
Marche 5	1	978	531	40
Marche 6	1	1 308	580	40
Marche 7	1	1 468	536	40
Marche 8	1	1 129	515	40
Marche 9	1	1 190	558	40
Marche 10	1	1 497	543	40
Marche 11	1	1 413	433	40
Marche 12	1	1 094	469	40
Marche 13	1	939	433	40
Contremarches 1, 2, 3, 4, 9, 14, 15, 16, 17	9	880	119	22
Contremarches 5, 13	2	895	119	22
Contremarches 6, 12	2	1 010	119	22
Contremarches 7, 11	2	1 325	119	22
Contremarche 8	1	1 041	119	22
Contremarche 10	1	1 281	119	22
Poteau	1	1 710	200	100

Cotes brutes de débit en millimètres, longueur dans le fil.

Volume brut débité : 0,669 m³ de chêne, soit environ 475 kg (710 kg/m³).


FABRICATION

- Tous les logements tiennent dans les limons, avec au moins 20 mm de bois dessous (limon de jour de 470 mm).
- Toutes les pièces tiennent dans un plateau de 5 000 × 600 mm.


Limons

Cotes en millimètres : nez depuis le bout gauche du plateau, hauteurs depuis sa rive basse, angles depuis sa rive. Logements défoncés de 15 mm, jeu de 0,5 mm par côté.

Limon de jour 1/2 2 136 × 571 × 45

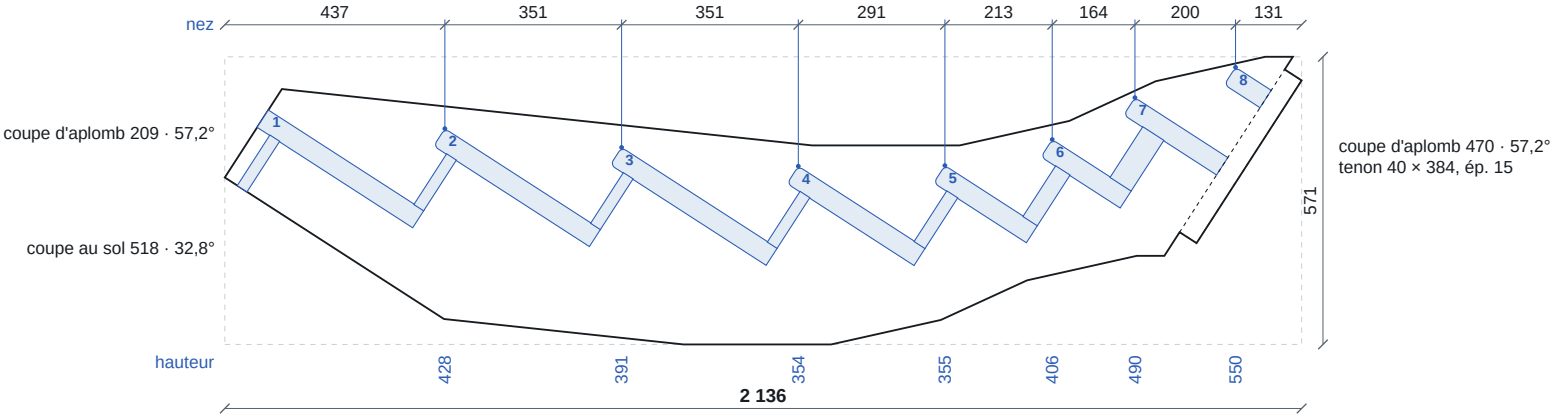

Limon de jour 2/2 2 278 × 571 × 45

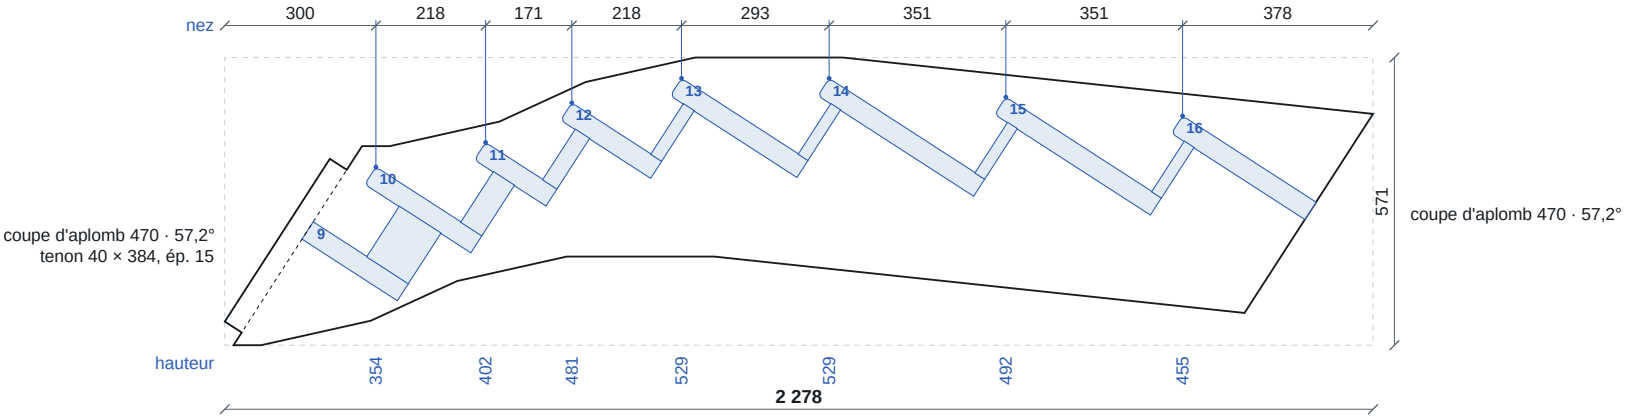


Limons

Vus côté marches, couchés dans le sens du plateau · échelle 1:15


Cotes en millimètres : nez depuis le bout gauche du plateau, hauteurs depuis sa rive basse, angles depuis sa rive. Logements défoncés de 15 mm, jeu de 0,5 mm par côté.

Limon de mur 1/3 2 895 × 461 × 45

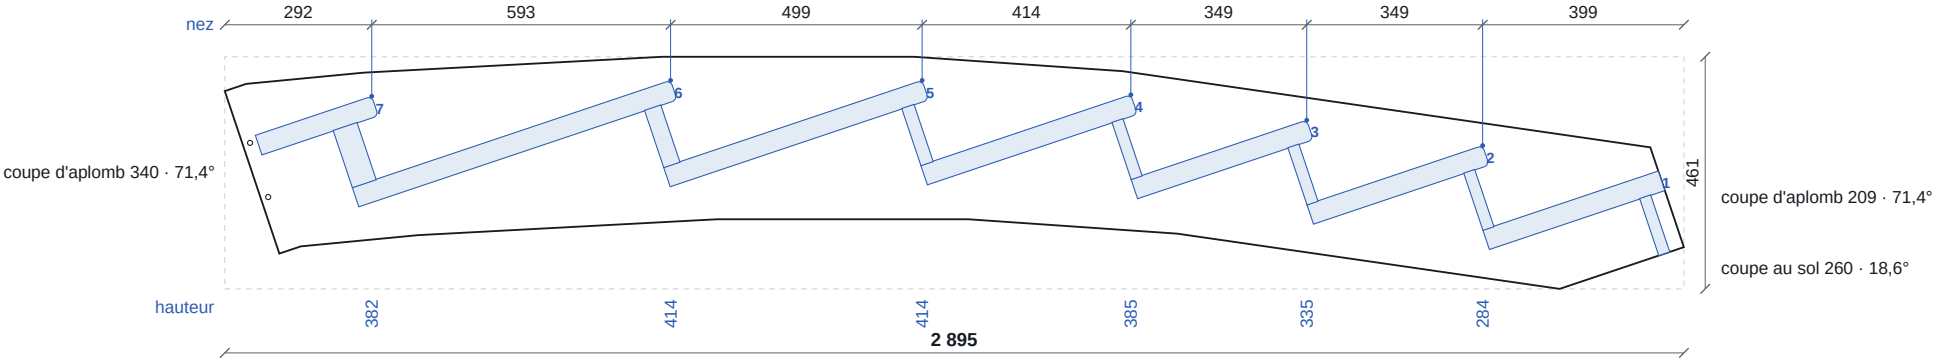

2 perçages Ø 10 traversants pour l'about du limon suivant : x 86, y 182 ; x 50, y 290.

Limon de mur 2/3 2 092 × 416 × 45

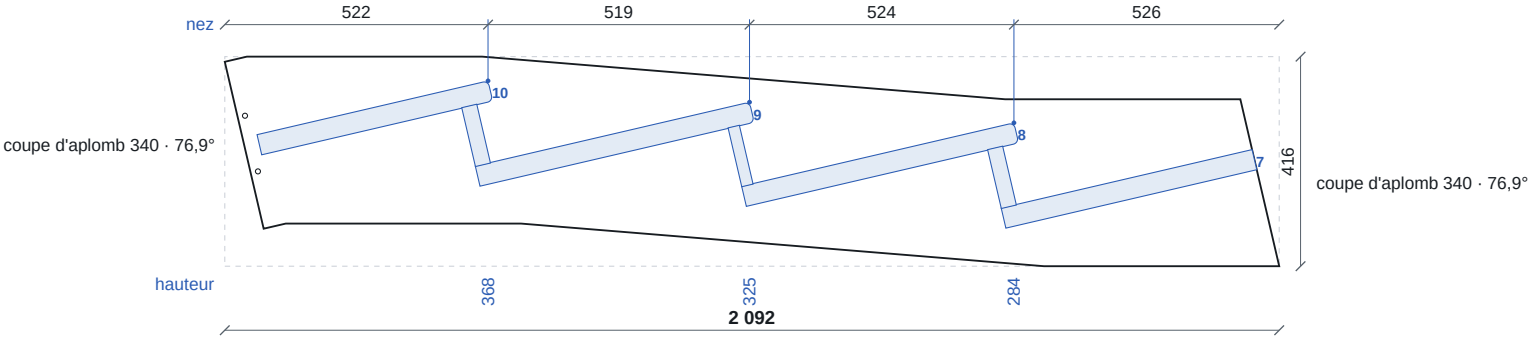

2 perçages Ø 10 traversants pour l'about du limon suivant : x 66, y 188 ; x 40, y 298.

Limons

Vus côté marches, couchés dans le sens du plateau · échelle 1:15

Cotes en millimètres : nez depuis le bout gauche du plateau, hauteurs depuis sa rive basse, angles depuis sa rive. Logements défoncés de 15 mm, jeu de 0,5 mm par côté.

Limon de mur 3/3 2 918 × 459 × 45

