Escalier quart-d

Escalier quart tournant droit · 15 hauteurs de 180,0 mm · giron 262,0 mm

COTES

Hauteur à monter	**2 700 mm**
Longueur côté départ	**2 900 mm**
Longueur côté arrivée	**1 800 mm**
Emmarchement	**850 mm**
Trémie	**2 550 mm × 1 845 mm**
Épaisseur du plancher	**200 mm**
Ligne de foulée (depuis le jour)	**425 mm**
Marches balancées	**7 · progressivité 60 %**
Tour	**marches 7 à 13 · 1 260 mm à 2 340 mm**

CONTRÔLES


Hauteur de marche	**180,0 mm**	**Bon**
Giron	**262,0 mm**	**Bon**
Blondel 2h + g	**622 mm**	**Bon**
Pente	**34,5 °**	**Bon**
Échappée jour	**2 049 mm**	**Bon**
Échappée foulée	**2 049 mm**	**Bon**
Échappée mur	**2 049 mm**	**Bon**
Giron mini au jour	**109 mm**	**Bon**

REMARQUES

- Escalier confortable : tout est dans les règles.
- Giron côté jour de 109 mm : au-dessus des 100 mm, mais beaucoup visent 120 à 150 mm au collet ; 8 marches balancées donnent 120 mm au moins.
- Trémie minimale pour 2 000 mm d'échappée : 2 480 mm côté départ, avec 1 845 mm côté arrivée.
- Pas de garde-corps : côté vide, il en faut un dès 1 m de chute (main courante à 900 mm au moins, NF P01-012). Rien à faire si l'escalier est entre deux murs ou si le garde-corps est posé à part.

Rouvrir cet escalier
sur quart-de-tour.fr

PLAN

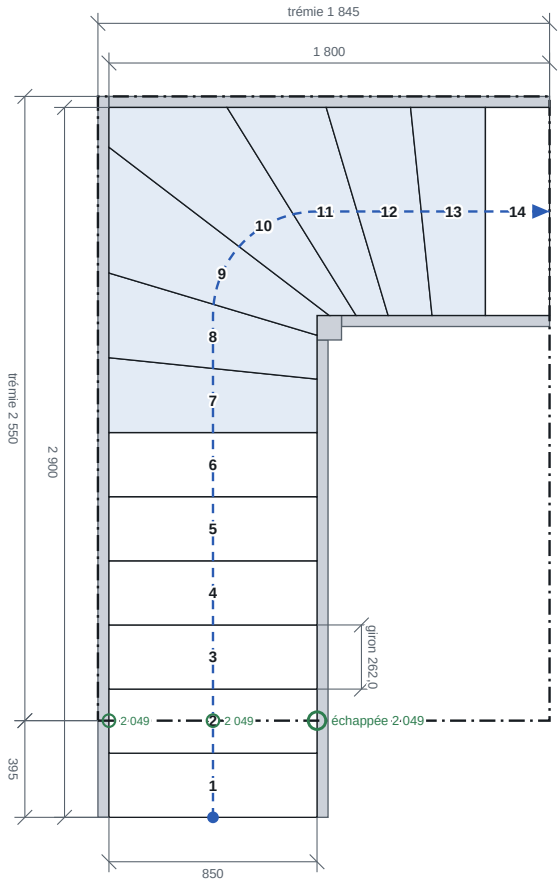

Bois et fiche des marches


BOIS

Essence	**Chêne**
Épaisseur de marche	**40 mm**
Débord de nez	**30 mm**
Profil du nez	**arrondi R10,0 dessus et dessous**
Contremarches	**22 mm, sur la marche**


LIMONS ET ASSEMBLAGE

Épaisseur de limon	**45 mm**
Hauteur du limon de mur	**340 mm**
Hauteur du limon de jour	**470 mm**
Section du poteau	**100 mm**
Encastrement	**15 mm**
Jeu d'assemblage par côté	**0,5 mm**
Garde-corps	**aucun**

VUE DE CÔTÉ, DÉVELOPPÉE SUR LA LIGNE DE FOULÉE

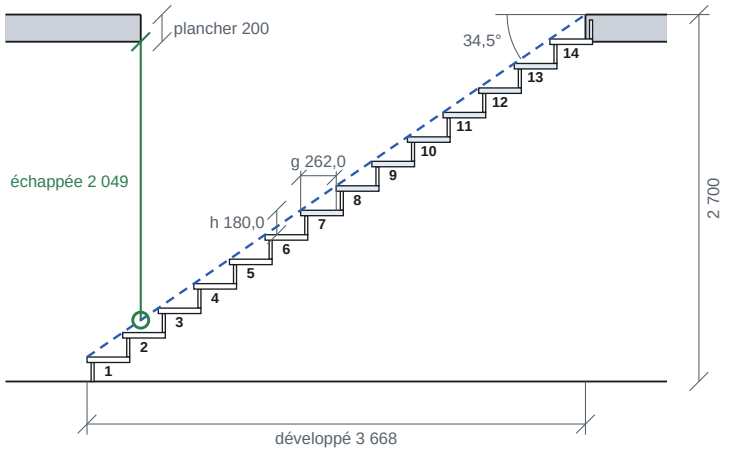

COUPE AU NEZ

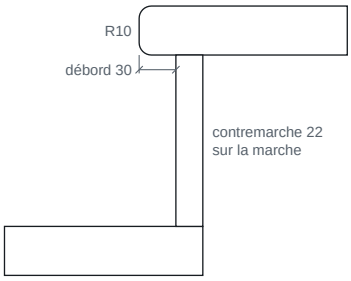

FICHE DES MARCHES

MARCHE	DESSUS	GIRON JOUR	GIRON FOULÉE	GIRON EXTÉRIEUR	LONGUEUR DE NEZ
1	180,0	262,0	262,0	262,0	850,0
2	360,0	262,0	262,0	262,0	850,0
3	540,0	262,0	262,0	262,0	850,0
4	720,0	262,0	262,0	262,0	850,0
5	900,0	262,0	262,0	262,0	850,0
6	1 080,0	262,0	262,0	262,0	850,0
7	1 260,0	218,2	262,0	305,8	850,0
8	1 440,0	179,3	262,0	345,9	854,5
9	1 620,0	130,9	262,0	514,1	887,2
10	1 800,0	109,4	262,0	644,8	1 132,8
11	1 980,0	130,9	262,0	405,2	1 000,2
12	2 160,0	179,3	262,0	344,6	886,8
13	2 340,0	218,2	262,0	305,8	854,5
14	2 520,0	262,0	262,0	262,0	850,0
Palier	2 700,0				

marches balancées · cotes en millimètres

Girons mesurés de nez à nez. Repères de confort usuels (Blondel 600 à 640 mm, hauteur 160 à 185 mm, giron d'au moins 240 mm, échappée d'au moins 2 000 mm et jamais sous 1 900 mm) : à confronter au NF DTU 36.3 et aux exigences du chantier avant fabrication.

Liste de débit

PIÈCE	QTÉ	LONGUEUR	LARGEUR	ÉPAISSEUR
Limon de jour 1/2	1	2 558	454	45
Limon de jour 2/2	1	1 520	418	45
Limon de mur 1/2	1	3 500	486	45
Limon de mur 2/2	1	2 130	434	45
Marches 1, 2, 3, 4, 5, 6, 14	7	880	314	40
Marche 7	1	880	360	40
Marche 8	1	927	401	40
Marche 9	1	1 202	562	40
Marche 10	1	1 405	466	40
Marche 11	1	1 131	395	40
Marche 12	1	984	384	40
Marche 13	1	913	358	40
Contremarches 1, 2, 3, 4, 5, 6, 7, 14, 15	9	880	140	22
Contremarches 8, 13	2	887	140	22
Contremarche 9	1	926	140	22
Contremarche 10	1	1 285	140	22
Contremarche 11	1	1 050	140	22
Contremarche 12	1	925	140	22
Poteau	1	2 040	100	100

Cotes brutes de débit en millimètres, longueur dans le fil.

Volume brut débité : 0,466 m³ de chêne, soit environ 330 kg (710 kg/m³).

FABRICATION


- Tous les logements tiennent dans les limons, avec au moins 20 mm de bois dessous (limon de jour de 470 mm).
- Toutes les pièces tiennent dans un plateau de 5 000 × 600 mm.

Limons


Vus côté marches, couchés dans le sens du plateau · échelle 1:20

Cotes en millimètres : nez depuis le bout gauche du plateau, hauteurs depuis sa rive basse, angles depuis sa rive. Logements défoncés de 15 mm, jeu de 0,5 mm par côté.


Limon de jour 1/2 2 558 × 454 × 45

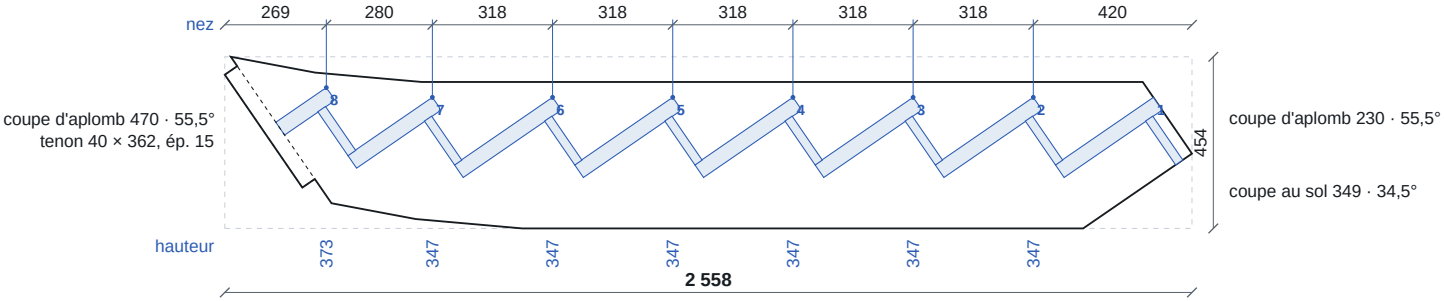

Limon de jour 2/2 1 520 × 418 × 45

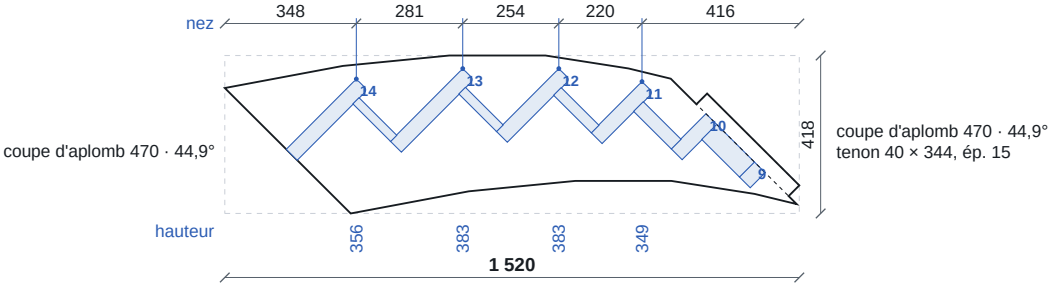

Limon de mur 1/2 3 500 × 486 × 45

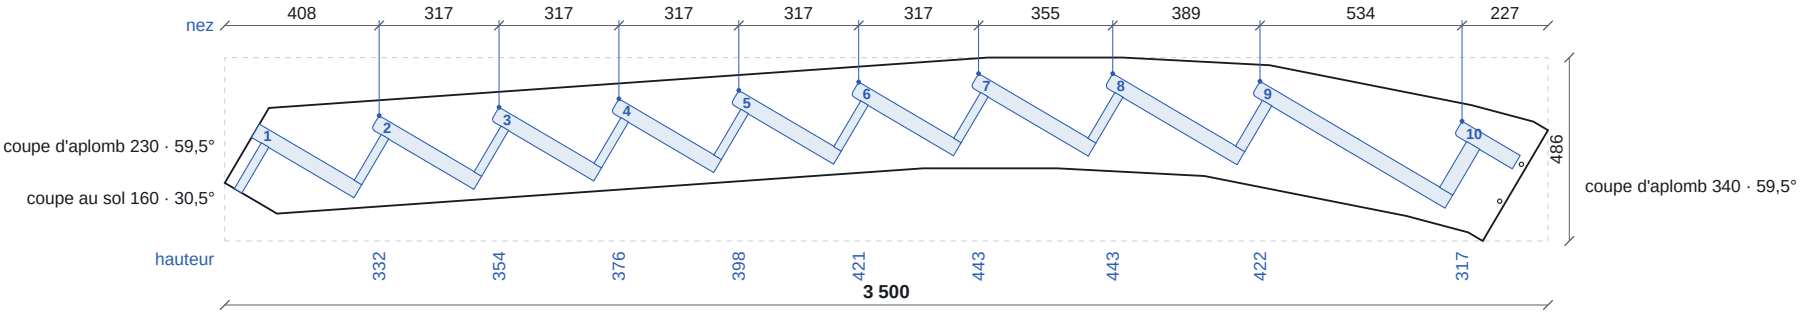

2 perçages Ø 10 traversants pour l'about du limon suivant : x 3 372, y 105 ; x 3 429, y 203.

Limons

Cotes en millimètres : nez depuis le bout gauche du plateau, hauteurs depuis sa rive basse, angles depuis sa rive. Logements défoncés de 15 mm, jeu de 0,5 mm par côté.

Limon de mur 2/2 2 130 × 434 × 45

