Escalier droit-palier

Escalier droit · 15 hauteurs de 180,0 mm · giron 260,7 mm

COTES

Hauteur à monter	**2 700 mm**
Reculement	**3 650 mm**
Emmarchement	**850 mm**
Trémie à prévoir	**3 490 mm**
Épaisseur du plancher	**200 mm**
Ligne de foulée (depuis le jour)	**425 mm**

CONTRÔLES


Hauteur de marche	**180,0 mm**	**Bon**
Giron	**260,7 mm**	**Bon**
Blondel 2h + g	**621 mm**	**Bon**
Pente	**34,6 °**	**Bon**
Échappée	**2 002 mm**	**Bon**
Reculement	**3 650 mm**	

REMARQUES

- Escalier confortable : tout est dans les règles.
- Trémie à prévoir pour 2 000 mm d'échappée : 3 490 mm de long.
- Garde-corps côté limon droit : main courante de 900 à 900 mm au-dessus des nez, 30 balustres, écart libre de 109 mm au plus.

Rouvrir cet escalier
sur quart-de-tour.fr

PLAN

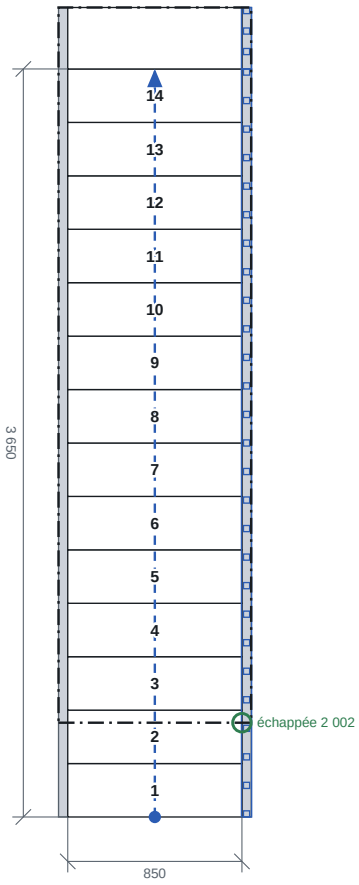

Bois et fiche des marches

BOIS

Essence	**Chêne**
Épaisseur de marche	**40 mm**
Débord de nez	**30 mm**
Rayon du nez	**10,0 mm**
Contremarches	**22 mm**
Marche palière	**300 × 50 mm**

LIMONS ET ASSEMBLAGE

Épaisseur de limon	**45 mm**
Hauteur de limon	**340 mm**
Encastrement	**15 mm**
Jeu d'assemblage par côté	**0,5 mm**
Garde-corps	**Balustres dans le chant**
Main courante	**50 × 70 mm**

FICHE DES MARCHES

MARCHE	DESSUS	GIRON	LONGUEUR DE NEZ
1	180,0	260,7	850,0
2	360,0	260,7	850,0
3	540,0	260,7	850,0
4	720,0	260,7	850,0
5	900,0	260,7	850,0
6	1 080,0	260,7	850,0
7	1 260,0	260,7	850,0
8	1 440,0	260,7	850,0
9	1 620,0	260,7	850,0
10	1 800,0	260,7	850,0
11	1 980,0	260,7	850,0
12	2 160,0	260,7	850,0
13	2 340,0	260,7	850,0
14	2 520,0	260,7	850,0
Palier	2 700,0		

Cotes en millimètres.

Girons mesurés de nez à nez. Repères de confort usuels (Blondel 600 à 640 mm, hauteur 160 à 185 mm, giron d'au moins 240 mm, échappée d'au moins 2 000 mm et jamais sous 1 900 mm) : à confronter au NF DTU 36.3 et aux exigences du chantier avant fabrication.

Liste de débit

PIÈCE	QTÉ	LONGUEUR	LARGEUR	ÉPAISSEUR
Limon droit	1	4 813	451	45
Limon gauche	1	4 813	451	45
Marches 1, 2, 3, 4, 5, 6, 7, 8, 9, 10, 11, 12, 13, 14	14	880	313	40
Marche palière	1	880	300	50
Contremarches 1, 2, 3, 4, 5, 6, 7, 8, 9, 10, 11, 12, 13, 14	14	880	140	22
Contremarche 15	1	880	130	22
Main courante	1	4 484	70	50
Retour de main courante	1	300	70	50
Balustres 1, 2, 3, 4, 5, 6, 7, 8, 9, 10, 11, 12, 13, 14, 15, 16, 17, 18, 19, 20, 21, 22, 23, 24, 25, 26, 27	27	1 005	30	30
Balustres 28, 29, 30	3	820	30	30

Cotes brutes de débit en millimètres, longueur dans le fil.

Volume brut débité : 0,441 m³ de chêne, soit environ 315 kg (710 kg/m³).

FABRICATION


- Tous les logements tiennent dans les limons, avec au moins 20 mm de bois dessous.
- Toutes les pièces tiennent dans un plateau de 5 000 × 600 mm.

Limons

Vus côté marches, couchés dans le sens du plateau · échelle 1:25

Cotes en millimètres : nez depuis le bout gauche du plateau, hauteurs depuis sa rive basse, angles depuis sa rive. Logements défoncés de 15 mm, jeu de 0,5 mm par côté.

Limon droit 4 813 × 451 × 45 · × 2 : le limon gauche est le même, retourné

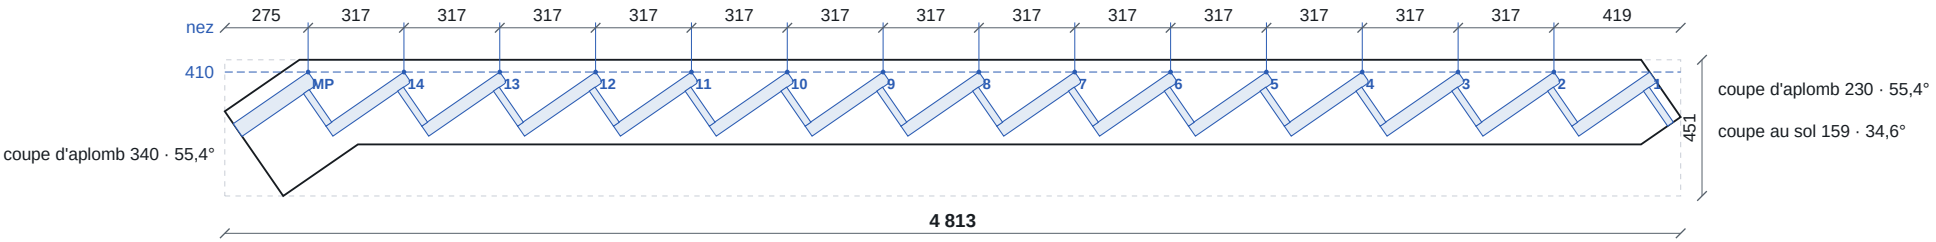

30 mortaises de balustres dans le chant haut.