Escalier droit-debordantes

Escalier droit · 15 hauteurs de 180,0 mm · giron 260,7 mm

COTES

Hauteur à monter	**2 700 mm**
Reculement	**3 650 mm**
Emmarchement	**850 mm**
Trémie	**3 200 mm**
Épaisseur du plancher	**200 mm**
Ligne de foulée (depuis le jour)	**425 mm**

CONTRÔLES


Hauteur de marche	**180,0 mm**	**Bon**
Giron	**260,7 mm**	**Bon**
Blondel 2h + g	**621 mm**	**Bon**
Pente	**34,6 °**	**Bon**
Échappée	**2 009 mm**	**Bon**
Reculement	**3 650 mm**	

REMARQUES

- Escalier confortable : tout est dans les règles.
- Trémie minimale pour 2 000 mm d'échappée : 3 190 mm de long.
- Pas de garde-corps : côté vide, il en faut un dès 1 m de chute (main courante à 900 mm au moins, NF P01-012). Rien à faire si l'escalier est entre deux murs ou si le garde-corps est posé à part.

Rouvrir cet escalier
sur quart-de-tour.fr

PLAN

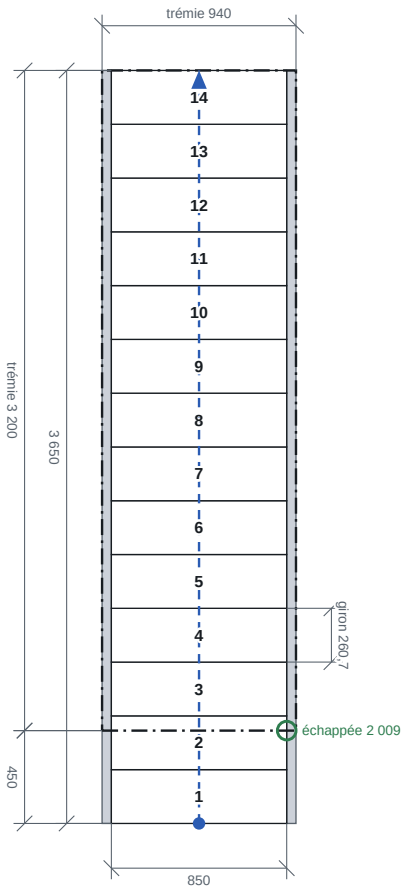

Bois et fiche des marches


BOIS

Essence	**Chêne**
Épaisseur de marche	**40 mm**
Débord de nez	**30 mm**
Profil du nez	**arrondi R10,0 dessus et dessous**
Contremarches	**22 mm, sur la marche**
Marches débordantes	**30 mm au jour**


LIMONS ET ASSEMBLAGE

Épaisseur de limon	**45 mm**
Hauteur du limon gauche	**340 mm**
Limon droit, en crémaillère	**420 mm**
Encastrement	**15 mm**
Jeu d'assemblage par côté	**0,5 mm**
Garde-corps	**aucun**

VUE DE CÔTÉ, DÉVELOPPÉE SUR LA LIGNE DE FOULÉE

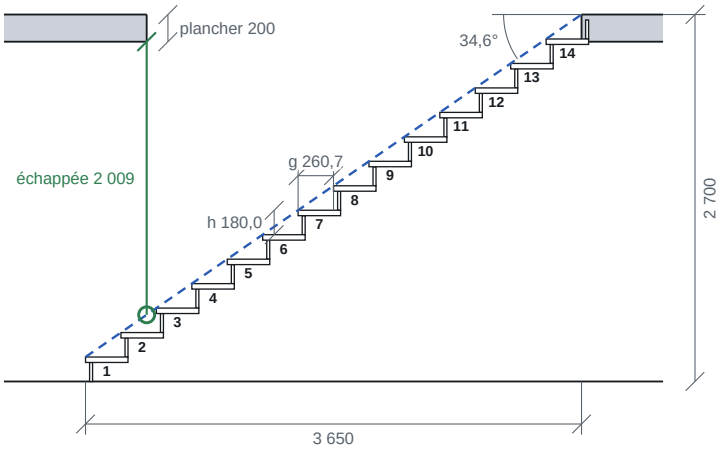

COUPE AU NEZ

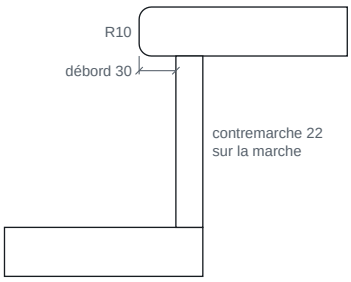

FICHE DES MARCHES

MARCHE	DESSUS	GIRON	LONGUEUR DE NEZ
1	180,0	260,7	850,0
2	360,0	260,7	850,0
3	540,0	260,7	850,0
4	720,0	260,7	850,0
5	900,0	260,7	850,0
6	1 080,0	260,7	850,0
7	1 260,0	260,7	850,0
8	1 440,0	260,7	850,0
9	1 620,0	260,7	850,0
10	1 800,0	260,7	850,0
11	1 980,0	260,7	850,0
12	2 160,0	260,7	850,0
13	2 340,0	260,7	850,0
14	2 520,0	260,7	850,0
Palier	2 700,0		

Cotes en millimètres.

Girons mesurés de nez à nez. Repères de confort usuels (Blondel 600 à 640 mm, hauteur 160 à 185 mm, giron d'au moins 240 mm, échappée d'au moins 2 000 mm et jamais sous 1 900 mm) : à confronter au NF DTU 36.3 et aux exigences du chantier avant fabrication.

Liste de débit

PIÈCE	QTÉ	LONGUEUR	LARGEUR	ÉPAISSEUR
Limon droit	1	4 370	243	45
Limon gauche	1	4 567	280	45
Marches 1, 2, 3, 4, 5, 6, 7, 8, 9, 10, 11, 12, 13, 14	14	940	313	40
Contremarches 1, 2, 3, 4, 5, 6, 7, 8, 9, 10, 11, 12, 13, 14, 15	15	910	140	22

Cotes brutes de débit en millimètres, longueur dans le fil.

Volume brut débité : 0,312 m³ de chêne, soit environ 220 kg (710 kg/m³).

FABRICATION


- Tous les logements tiennent dans les limons, avec au moins 20 mm de bois dessous.
- Toutes les pièces tiennent dans un plateau de 5 000 × 600 mm.

Limons


Escalier droit-debordantes
Vus côté marches, couchés dans le sens du plateau · échelle 1:25

Cotes en millimètres : nez depuis le bout gauche du plateau, hauteurs depuis sa rive basse, angles depuis sa rive. Logements défoncés de 15 mm, jeu de 0,5 mm par côté. Points a, b, c… : voir le traçage à la main.

Limon droit 4 370 × 243 × 45

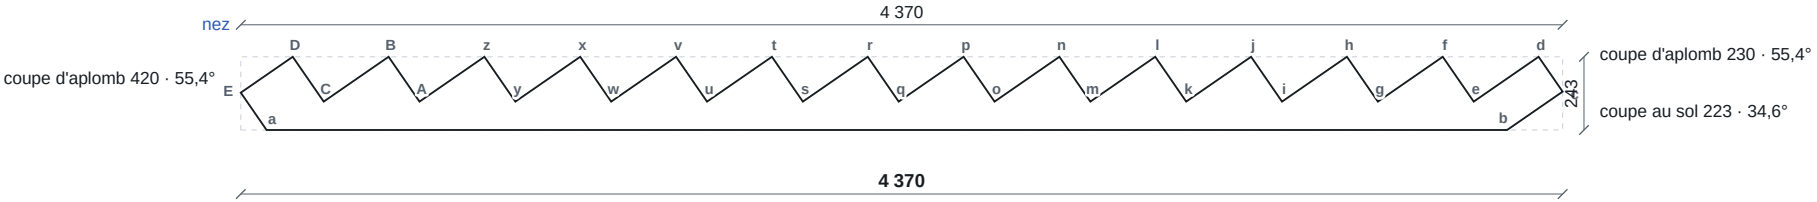

Limon gauche 4 567 × 280 × 45

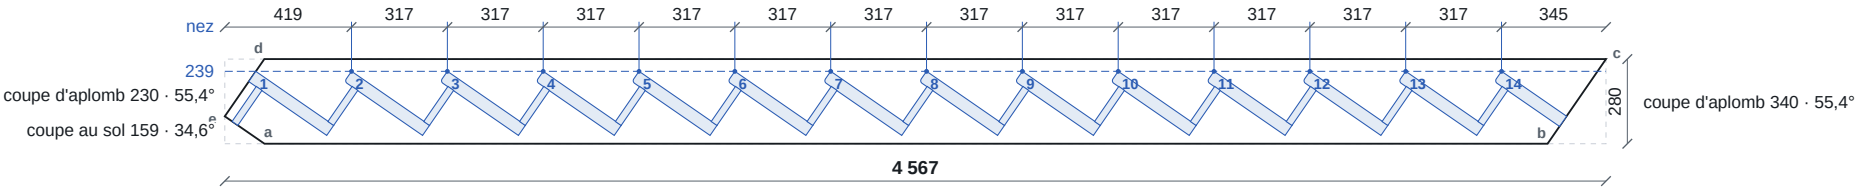

Traçage des limons

1. Dresser la rive basse du plateau et tracer le bout gauche d'équerre : x se mesure le long de la rive depuis ce bout, y d'équerre depuis la rive.
2. Contour : pointer a, b, c… et les joindre dans l'ordre. Les lettres sont aussi sur le dessin des limons.
3. Marches : pointer le nez et le fond, les joindre, c'est le dessus de la marche ; tracer le dessous parallèle, 41 mm plus bas (marche et jeu). Arrondir le bout côté nez au rayon 10.
4. Contremarches : sur le dessus de la marche, depuis le nez, pointer les deux distances données ; tracer d'équerre vers le bas jusqu'au dessus de la marche d'en dessous, ou jusqu'au sol.
5. Défoncer à 15 mm. Tous les dessus de marche d'un limon sont parallèles : la fausse équerre réglée comme indiqué les contrôle.

Limon droit

4 370 × 243 × 45 · dessus de marche à 34,6° sur la rive, montant vers la droite (fausse équerre : 1 000 le long de la rive, 690 d'équerre)

	Nez		Fond		Contremarche, depuis le nez	
Marche	x	y	x	y	de	à

Contour		
Point	x	y
a	85	0
b	4 186	0
c	4 370	127
d	4 290	242
e	4 076	94
f	3 974	242
g	3 759	94
h	3 657	242
i	3 442	94
j	3 340	242
k	3 125	94

Point	x	y
l	3 023	242
m	2 809	94
n	2 706	242
o	2 492	94
p	2 389	242
q	2 175	94
r	2 073	242
s	1 858	94
t	1 756	242
u	1 541	94
v	1 439	242

Point	x	y
w	1 224	94
x	1 122	242
y	908	94
z	805	242
A	591	94
B	489	242
C	274	94
D	172	242
E	0	123

Limon gauche

4 567 × 280 × 45 · dessus de marche à 34,6° sur la rive, descendant vers la droite (fausse équerre : 1 000 le long de la rive, 690 d'équerre)

	Nez		Fond		Contremarche, depuis le nez	
Marche	x	y	x	y	de	à
1 *	103	239	360	61	30	53
2	419	239	677	61	30	53
3	736	239	994	61	30	53
4	1 053	239	1 311	61	30	53
5	1 369	239	1 628	61	30	53
6	1 686	239	1 944	61	30	53
7	2 003	239	2 261	61	30	53
8	2 320	239	2 578	61	30	53
9	2 637	239	2 895	61	30	53
10	2 953	239	3 212	61	30	53
11	3 270	239	3 528	61	30	53
12	3 587	239	3 845	61	30	53
13	3 904	239	4 162	61	30	53
14	4 221	239	4 436	91	30	53

* logement coupé par l'about : le point « nez » est pris sur l'about.

Contour		
Point	x	y
a	131	0
b	4 373	0

Point	x	y
c	4 566	280
d	131	280

Point	x	y
e	0	91