Escalier demi-g-large

Escalier demi-tournant gauche · 17 hauteurs de 158,8 mm · giron 327,2 mm

COTES

Hauteur à monter	**2 700 mm**
Longueur côté départ	**2 600 mm**
Jour, limons compris	**400 mm**
Longueur côté arrivée	**2 600 mm**
Emmarchement	**850 mm**
Trémie	**2 650 mm × 2 190 mm**
Épaisseur du plancher	**200 mm**
Ligne de foulée (depuis le jour)	**425 mm**
Marches balancées	**5 et 5 · progressivité 60 %**
Premier tour	**marches 4 à 8 · 635 mm à 1 271 mm**
Second tour	**marches 9 à 13 · 1 429 mm à 2 065 mm**

CONTRÔLES


Hauteur de marche	**158,8 mm**	**Bon**
Giron	**327,2 mm**	**Limite**
Blondel 2h + g	**645 mm**	**Limite**
Pente	**25,9 °**	**Bon**
Échappée jour	**Libre**	**Bon**
Échappée foulée	**Libre**	**Bon**
Échappée mur	**Libre**	**Bon**
Giron mini au jour	**114 mm**	**Bon**

REMARQUES

- Giron long (327 mm) : ajoutez une hauteur pour un pas plus naturel.
- Loi de Blondel hors plage : 2h + g = 645 mm, visez 600 à 640 mm.
- Longueur côté départ conseillée : 2 480 mm, soit 17 hauteurs de 158,8 mm et un giron de 319,7 mm.
- Trémie minimale pour 2 000 mm d'échappée : 2 610 mm côté arrivée, avec 2 190 mm côté fond.
- Garde-corps : main courante de 900 à 1 071 mm au-dessus des nez, 4 montants et 29 lisses, écart libre de 103 mm au plus.
- La lisse basse touche le limon là où il monte plus vite que la main courante (tournant) : préférez des balustres.

Rouvrir cet escalier
sur quart-de-tour.fr

PLAN

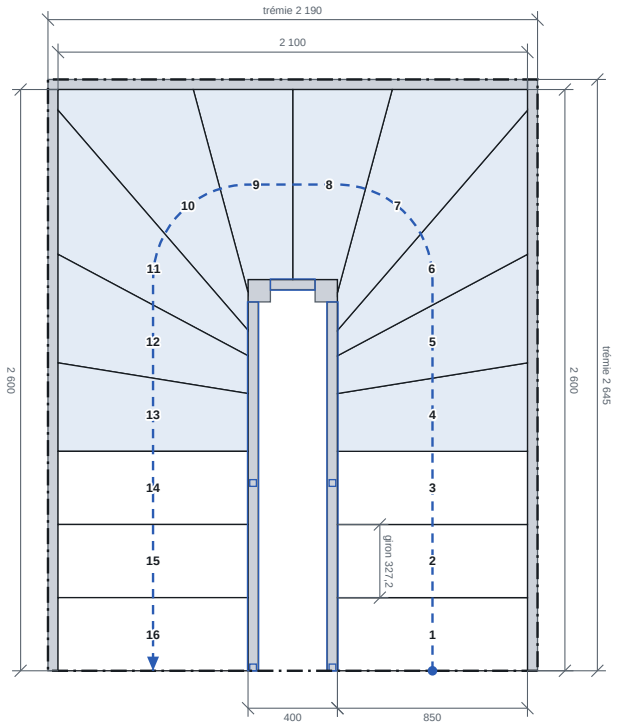

Bois et fiche des marches


BOIS

Essence	**Chêne**
Épaisseur de marche	**40 mm**
Débord de nez	**30 mm**
Profil du nez	**arrondi R10,0 dessus et dessous**
Contremarches	**22 mm, sur la marche**

LIMONS ET ASSEMBLAGE


Épaisseur de limon	**45 mm**
Hauteur du limon de mur	**340 mm**
Hauteur du limon de jour	**550 mm**
Section du poteau	**100 mm**
Encastrement	**15 mm**
Jeu d'assemblage par côté	**0,5 mm**
Garde-corps	**Lisses rampantes dans le chant**
Main courante	**50 × 70 mm**

VUE DE CÔTÉ, DÉVELOPPÉE SUR LA LIGNE DE FOULÉE

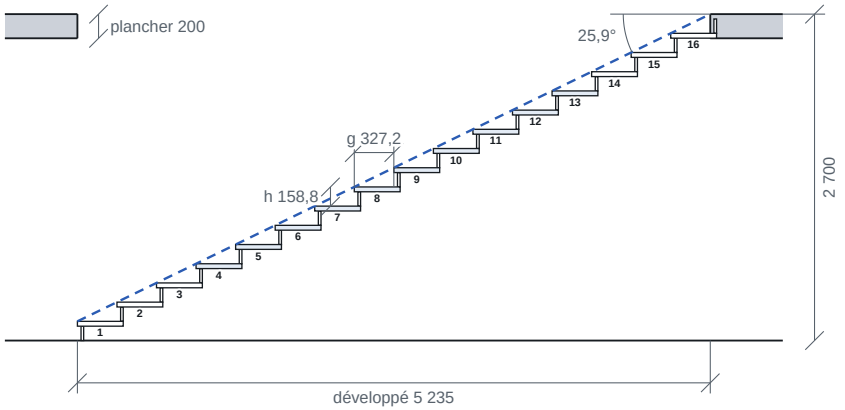

Échappée libre : tout l'escalier passe sous la trémie.

COUPE AU NEZ

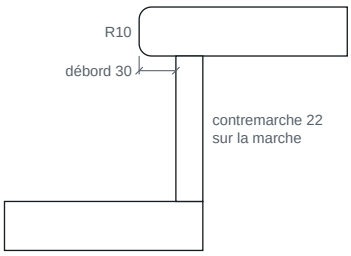

FICHE DES MARCHES

MARCHE	DESSUS	GIRON JOUR	GIRON FOULÉE	GIRON EXTÉRIEUR	LONGUEUR DE NEZ
1	158,8	327,2	327,2	327,2	850,0
2	317,6	327,2	327,2	327,2	850,0
3	476,5	327,2	327,2	327,2	850,0
4	635,3	258,5	327,2	395,9	850,0
5	794,1	168,9	327,2	485,5	861,0
6	952,9	113,6	327,2	644,5	963,6
7	1 111,8	168,9	327,2	697,5	1 301,0
8	1 270,6	258,5	327,2	445,0	941,0
9	1 429,4	258,5	327,2	445,0	850,0
10	1 588,2	168,9	327,2	697,5	941,0
11	1 747,1	113,6	327,2	644,5	1 301,0
12	1 905,9	168,9	327,2	485,5	963,6
13	2 064,7	258,5	327,2	395,9	861,0
14	2 223,5	327,2	327,2	327,2	850,0
15	2 382,4	327,2	327,2	327,2	850,0
16	2 541,2	327,2	327,2	327,2	850,0
Palier	2 700,0				

marches balancées · cotes en millimètres

Girons mesurés de nez à nez. Repères de confort usuels (Blondel 600 à 640 mm, hauteur 160 à 185 mm, giron d'au moins 240 mm, échappée d'au moins 2 000 mm et jamais sous 1 900 mm) : à confronter au NF DTU 36.3 et aux exigences du chantier avant fabrication.

Liste de débit

PIÈCE	QTÉ	LONGUEUR	LARGEUR	ÉPAISSEUR
Limon de jour 1/3	1	2 096	627	45
Limon de jour 2/3	1	280	673	45
Limon de jour 3/3	1	2 274	627	45
Limon de mur 1/3	1	2 882	458	45
Limon de mur 2/3	1	2 299	444	45
Limon de mur 3/3	1	2 903	457	45
Marches 1, 2, 3, 14, 15, 16	6	880	380	40
Marche 4	1	880	452	40
Marche 5	1	980	543	40
Marche 6	1	1 344	647	40
Marche 7	1	1 416	566	40
Marche 8	1	1 015	484	40
Marche 9	1	1 179	503	40
Marche 10	1	1 378	639	40
Marche 11	1	1 471	466	40
Marche 12	1	1 100	480	40
Marche 13	1	941	445	40
Contremarches 1, 2, 3, 4, 9, 14, 15, 16, 17	9	880	119	22
Contremarches 5, 13	2	895	119	22
Contremarches 6, 12	2	1 010	119	22
Contremarches 7, 11	2	1 373	119	22
Contremarche 8	1	918	119	22
Contremarche 10	1	1 221	119	22
Main courante 1/3	1	2 034	70	50
Main courante 2/3	1	319	70	50
Main courante 3/3	1	2 034	70	50
Montant 1	1	809	30	30
Montant 2	1	945	30	30
Montant 3	1	840	30	30
Montant 4	1	975	30	30
Lisses 1, 2, 3, 4, 5, 6, 7, 8, 9, 10, 11, 12, 18, 19, 20, 21, 22, 23, 24, 25, 26, 27, 28, 29	24	968	30	30
Lisses 13, 14, 15, 16, 17	5	254	30	30
Poteau 1	1	2 330	100	100
Poteau 2	1	2 760	100	100

Cotes brutes de débit en millimètres, longueur dans le fil.

Volume brut débité : 0,759 m³ de chêne, soit environ 540 kg (710 kg/m³).

FABRICATION


- Tous les logements tiennent dans les limons, avec au moins 20 mm de bois dessous (limon de jour de 550 mm).
- Marches 6, 10 plus profondes que le plateau (jusqu'à 647 mm pour 600) : à reconstituer en lames collées, fil le long du nez.
- Limon de jour 1/3 (2 096 × 627 mm) plus grand que le plateau de 5 000 × 600 mm : à abouter ou à débiter dans un plateau plus grand.
- Limon de jour 2/3 (280 × 673 mm) plus grand que le plateau de 5 000 × 600 mm : à abouter ou à débiter dans un plateau plus grand.
- Limon de jour 3/3 (2 274 × 627 mm) plus grand que le plateau de 5 000 × 600 mm : à abouter ou à débiter dans un plateau plus grand.

Limons

Escalier demi-g-large
Vus côté marches, couchés dans le sens du plateau · échelle 1:15


Cotes en millimètres : nez depuis le bout gauche du plateau, hauteurs depuis sa rive basse, angles depuis sa rive. Logements défoncés de 15 mm, jeu de 0,5 mm par côté.

Limon de jour 1/3 2 096 × 627 × 45

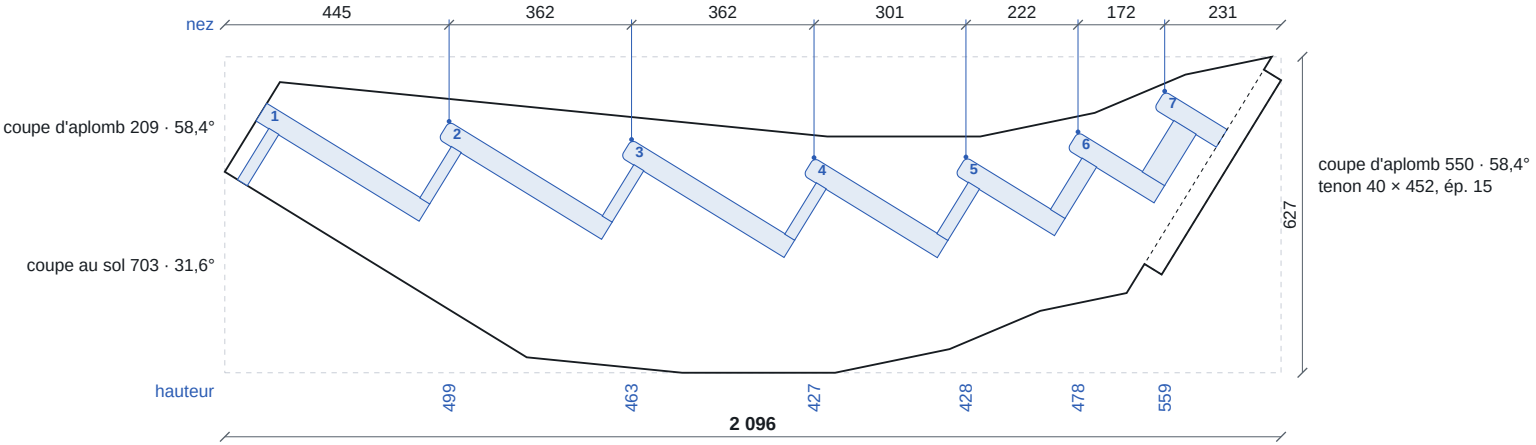

2 mortaises de balustres dans le chant haut.

Limon de jour 2/3 280 × 673 × 45

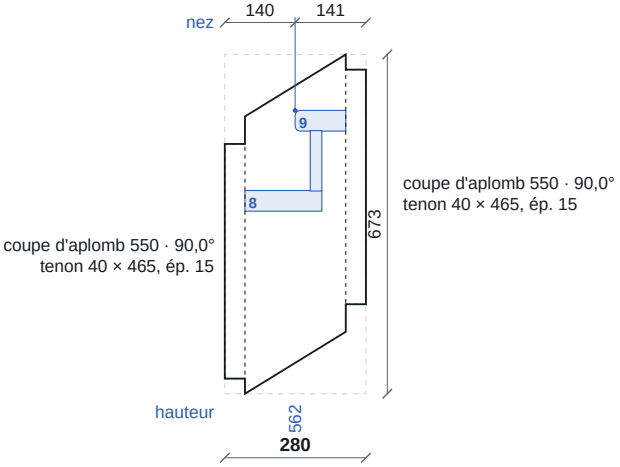


Limons

Escalier demi-g-large
Vus côté marches, couchés dans le sens du plateau · échelle 1:15


Cotes en millimètres : nez depuis le bout gauche du plateau, hauteurs depuis sa rive basse, angles depuis sa rive. Logements défoncés de 15 mm, jeu de 0,5 mm par côté.

Limon de jour 3/3 2 274 × 627 × 45

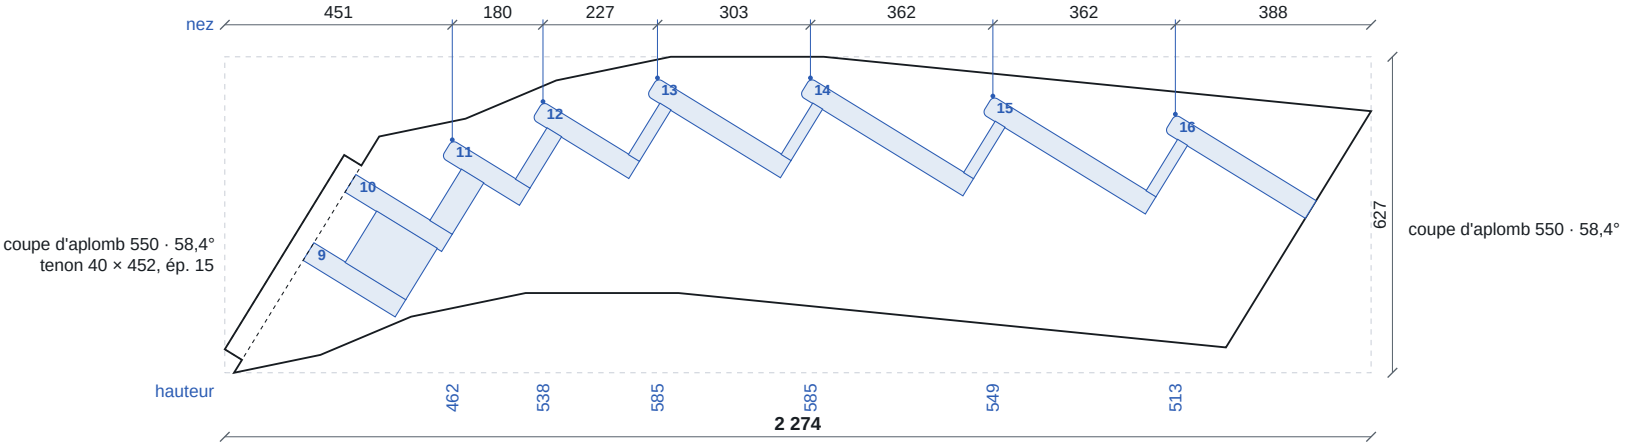

2 mortaises de balustres dans le chant haut.

Limon de mur 1/3 2 882 × 458 × 45

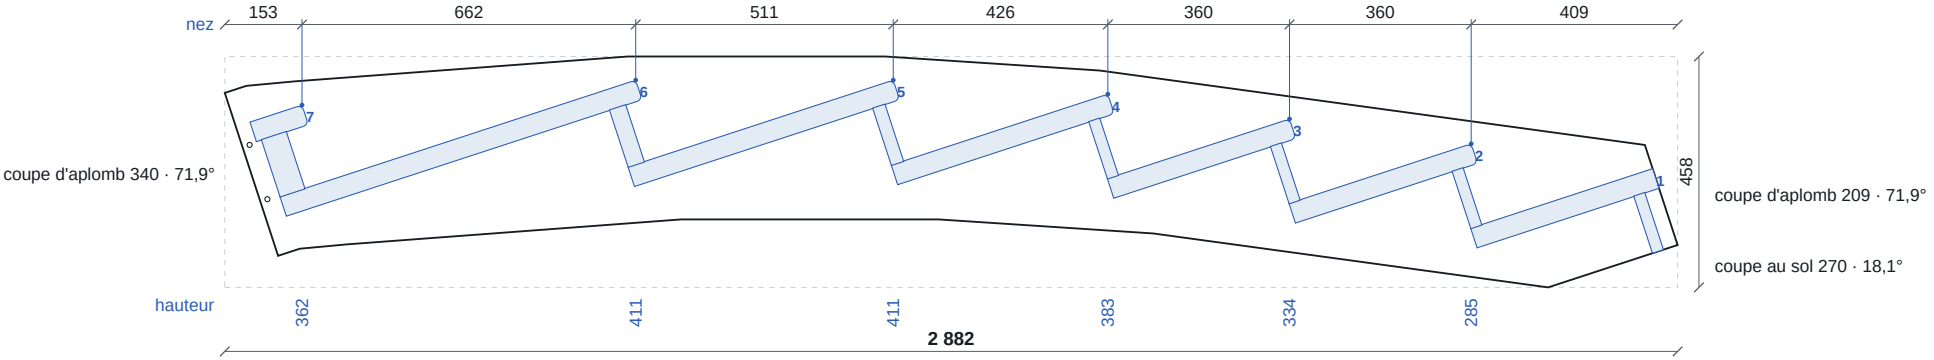


2 perçages Ø 10 traversants pour l'about du limon suivant : x 84, y 175 ; x 49, y 283.

Limons

Cotes en millimètres : nez depuis le bout gauche du plateau, hauteurs depuis sa rive basse, angles depuis sa rive. Logements défoncés de 15 mm, jeu de 0,5 mm par côté.

Limon de mur 2/3 2 299 × 444 × 45

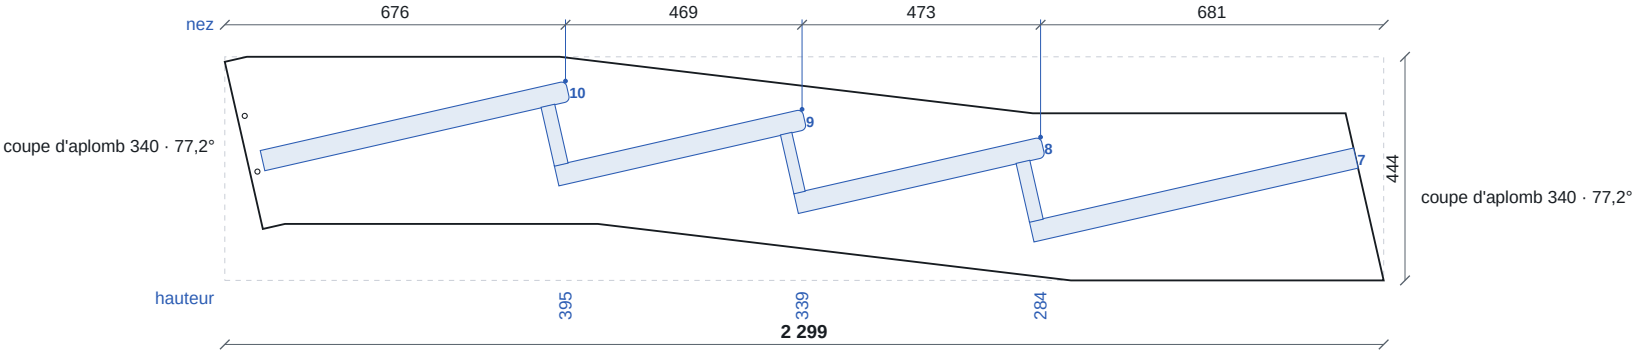

2 perçages Ø 10 traversants pour l'about du limon suivant : x 65, y 216 ; x 40, y 326.

Limon de mur 3/3 2 903 × 457 × 45

