# Escalier quart-d-chanfrein-rainures

Escalier quart tournant droit · 15 hauteurs de 180,0 mm · giron 262,0 mm

## COTES

| | |
|---|---|
| Hauteur à monter | **2 700 mm** |
| Longueur côté départ | **2 900 mm** |
| Longueur côté arrivée | **1 800 mm** |
| Emmarchement | **850 mm** |
| Trémie | **2 550 mm × 1 845 mm** |
| Épaisseur du plancher | **200 mm** |
| Ligne de foulée (depuis le jour) | **425 mm** |
| Marches balancées | **7 · progressivité 60 %** |
| Tour | **marches 7 à 13 · 1 260 mm à 2 340 mm** |

## CONTRÔLES


| | | |
|---|---|---|
| Hauteur de marche | **180,0 mm** | **Bon** |
| Giron | **262,0 mm** | **Bon** |
| Blondel 2h + g | **622 mm** | **Bon** |
| Pente | **34,5 °** | **Bon** |
| Échappée jour | **2 049 mm** | **Bon** |
| Échappée foulée | **2 049 mm** | **Bon** |
| Échappée mur | **583 mm** | **Hors norme** |
| Giron mini au jour | **109 mm** | **Bon** |

## REMARQUES

- Échappée de 583 mm côté mur, au-dessus de la marche 10 (2 049 mm sur la ligne de foulée) : pour 2 000 mm, allongez la trémie côté arrivée à 2 110 mm.

**Rouvrir cet escalier**
sur quart-de-tour.fr

## PLAN

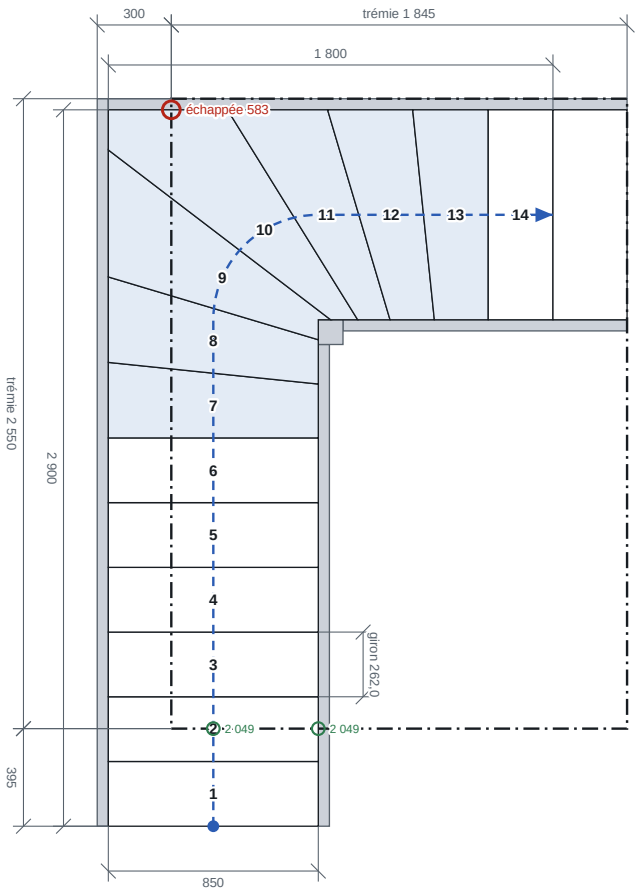

# Bois et fiche des marches


### BOIS

| | |
|---|---|
| Essence | **Chêne** |
| Épaisseur de marche | **40 mm** |
| Débord de nez | **30 mm** |
| Profil du nez | **chanfrein 8,0 mm à 45°, dessous vif** |
| Rainures antidérapantes | **3 de 6 × 3 mm, entraxe 14** |
| Première rainure | **axe à 22 mm du nez** |
| Contremarches | **22 mm, sur la marche** |
| Embrèvement sous la marche | **6 mm** |
| Marche palière | **300 × 40 mm** |

### LIMONS ET ASSEMBLAGE


| | |
|---|---|
| Épaisseur de limon | **45 mm** |
| Hauteur du limon de mur | **340 mm** |
| Hauteur du limon de jour | **470 mm** |
| Section du poteau | **100 mm** |
| Encastrement | **15 mm** |
| Jeu d'assemblage par côté | **0,5 mm** |
| Garde-corps | **aucun** |

### VUE DE CÔTÉ, DÉVELOPPÉE SUR LA LIGNE DE FOULÉE

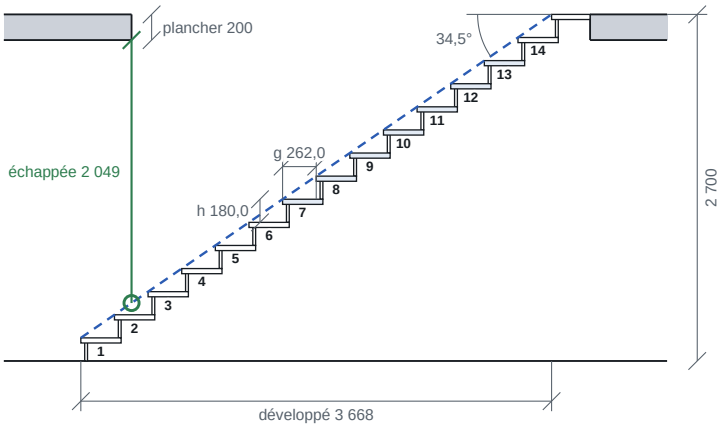


Échappée la plus faible : 583 mm côté mur, sur la marche 10.

### COUPE AU NEZ

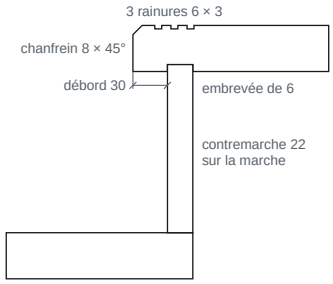


### FICHE DES MARCHES

| MARCHE | DESSUS | GIRON JOUR | GIRON FOULÉE | GIRON EXTÉRIEUR | LONGUEUR DE NEZ |
|---|---|---|---|---|---|
| 1 | 180,0 | 262,0 | 262,0 | 262,0 | 850,0 |
| 2 | 360,0 | 262,0 | 262,0 | 262,0 | 850,0 |
| 3 | 540,0 | 262,0 | 262,0 | 262,0 | 850,0 |
| 4 | 720,0 | 262,0 | 262,0 | 262,0 | 850,0 |
| 5 | 900,0 | 262,0 | 262,0 | 262,0 | 850,0 |
| 6 | 1 080,0 | 262,0 | 262,0 | 262,0 | 850,0 |
| 7 | 1 260,0 | 218,2 | 262,0 | 305,8 | 850,0 |
| 8 | 1 440,0 | 179,3 | 262,0 | 345,9 | 854,5 |
| 9 | 1 620,0 | 130,9 | 262,0 | 514,1 | 887,2 |
| 10 | 1 800,0 | 109,4 | 262,0 | 644,8 | 1 132,8 |
| 11 | 1 980,0 | 130,9 | 262,0 | 405,2 | 1 000,2 |
| 12 | 2 160,0 | 179,3 | 262,0 | 344,6 | 886,8 |
| 13 | 2 340,0 | 218,2 | 262,0 | 305,8 | 854,5 |
| 14 | 2 520,0 | 262,0 | 262,0 | 262,0 | 850,0 |
| Palier | 2 700,0 | | | | |

marches balancées · cotes en millimètres

Girons mesurés de nez à nez. Repères de confort usuels (Blondel 600 à 640 mm, hauteur 160 à 185 mm, giron d'au moins 240 mm, échappée d'au moins 2 000 mm et jamais sous 1 900 mm) : à confronter au NF DTU 36.3 et aux exigences du chantier avant fabrication.

# Liste de débit

| PIÈCE | QTÉ | LONGUEUR | LARGEUR | ÉPAISSEUR |
|---|---|---|---|---|
| Limon de jour 1/2 | 1 | 2 558 | 454 | 45 |
| Limon de jour 2/2 | 1 | 1 694 | 581 | 45 |
| Limon de mur 1/2 | 1 | 3 500 | 486 | 45 |
| Limon de mur 2/2 | 1 | 2 405 | 434 | 45 |
| Marches 1, 2, 3, 4, 5, 6, 14 | 7 | 880 | 314 | 40 |
| Marche 7 | 1 | 880 | 360 | 40 |
| Marche 8 | 1 | 927 | 401 | 40 |
| Marche 9 | 1 | 1 202 | 562 | 40 |
| Marche 10 | 1 | 1 405 | 466 | 40 |
| Marche 11 | 1 | 1 131 | 395 | 40 |
| Marche 12 | 1 | 984 | 384 | 40 |
| Marche 13 | 1 | 913 | 358 | 40 |
| Marche palière | 1 | 880 | 300 | 40 |
| Contremarches 1, 2, 3, 4, 5, 6, 7, 14, 15 | 9 | 880 | 146 | 22 |
| Contremarches 8, 13 | 2 | 887 | 146 | 22 |
| Contremarche 9 | 1 | 926 | 146 | 22 |
| Contremarche 10 | 1 | 1 285 | 146 | 22 |
| Contremarche 11 | 1 | 1 050 | 146 | 22 |
| Contremarche 12 | 1 | 925 | 146 | 22 |
| Poteau | 1 | 2 040 | 100 | 100 |

Cotes brutes de débit en millimètres, longueur dans le fil.

**Volume brut débité : 0,499 m³ de chêne, soit environ 355 kg (710 kg/m³).**


### FABRICATION

- Tous les logements tiennent dans les limons, avec au moins 20 mm de bois dessous (limon de jour de 470 mm).
- Toutes les pièces tiennent dans un plateau de 5 000 × 600 mm.


# Limons

Cotes en millimètres : nez depuis le bout gauche du plateau, hauteurs depuis sa rive basse, angles depuis sa rive. Logements défoncés de 15 mm, jeu de 0,5 mm par côté.

## Limon de jour 1/2 2 558 × 454 × 45

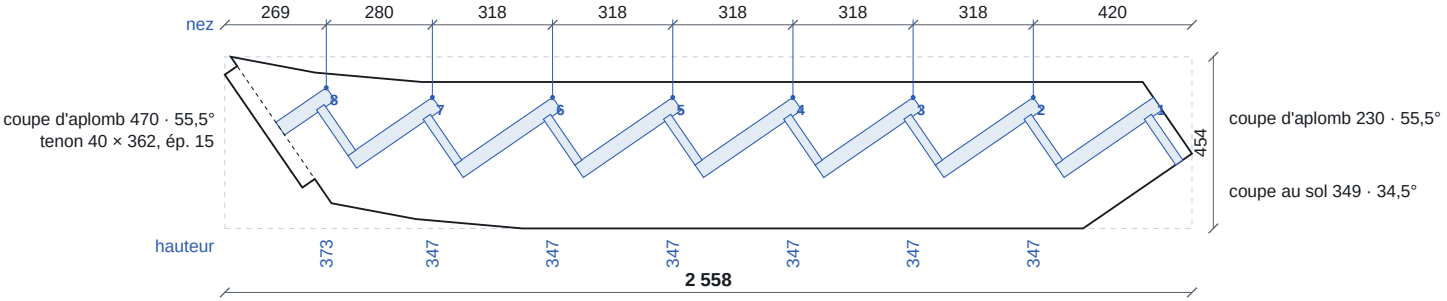


## Limon de jour 2/2 1 694 × 581 × 45

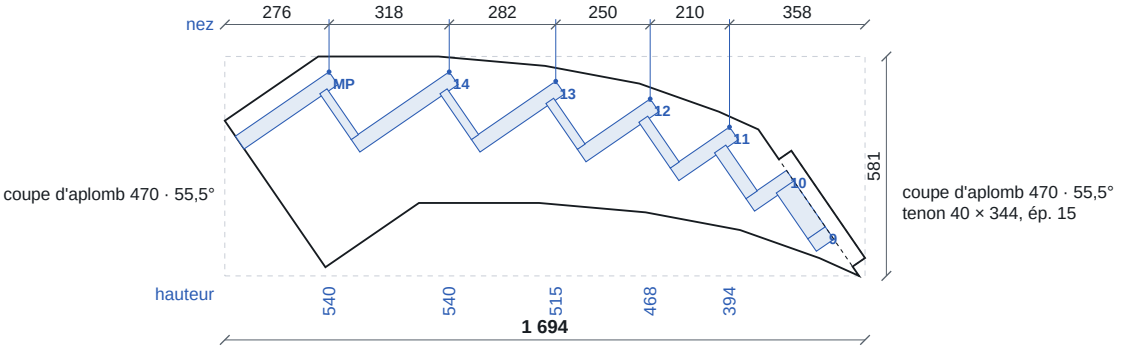


# Limons

Escalier quart-d-chanfrein-rainures
Vus côté marches, couchés dans le sens du plateau · échelle 1:20

Cotes en millimètres : nez depuis le bout gauche du plateau, hauteurs depuis sa rive basse, angles depuis sa rive. Logements défoncés de 15 mm, jeu de 0,5 mm par côté.

## Limon de mur 1/2 3 500 × 486 × 45

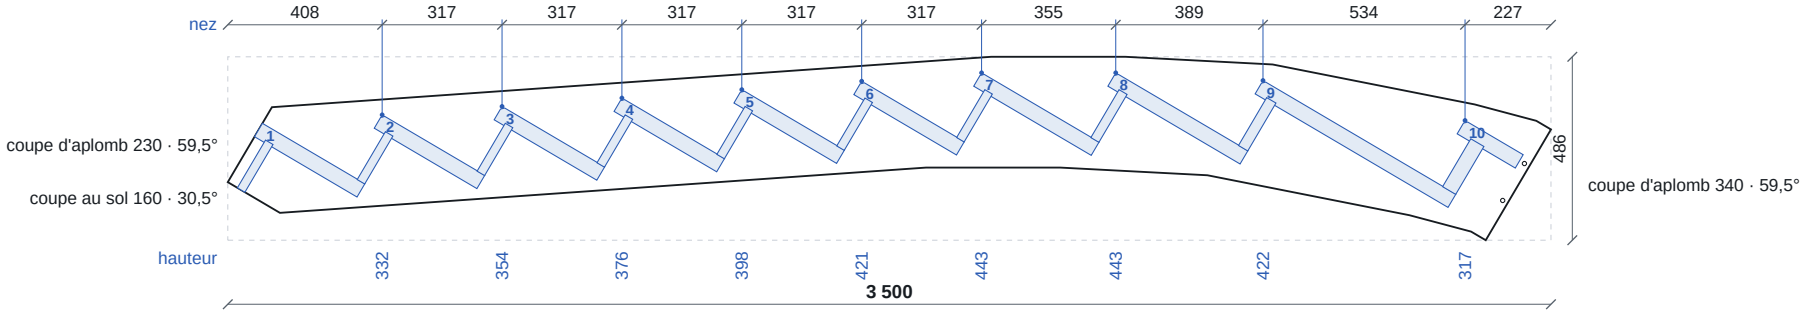


2 perçages Ø 10 traversants pour l'about du limon suivant : x 3 372, y 105 ; x 3 429, y 203.

## Limon de mur 2/2 2 405 × 434 × 45

