Escalier quart-g-a-palier-balustres

Escalier quart tournant gauche · 15 hauteurs de 180,0 mm · giron 264,3 mm

COTES

Hauteur à monter	**2 700 mm**
Longueur côté départ	**2 550 mm**
Longueur côté arrivée	**2 700 mm**
Emmarchement	**850 mm**
Trémie à prévoir	**2 130 mm × 2 745 mm**
Épaisseur du plancher	**200 mm**
Ligne de foulée (depuis le jour)	**425 mm**
Palier	**marche 7 · 964 mm de profondeur**

CONTRÔLES


Hauteur de marche	**180,0 mm**	Bon
Giron	**264,3 mm**	Bon
Blondel 2h + g	**624 mm**	Bon
Pente	**34,3 °**	Bon
Échappée jour	**2 003 mm**	Bon
Échappée foulée	**2 003 mm**	Bon
Échappée mur	**2 003 mm**	Bon
Palier	**964 mm**	

REMARQUES

- Escalier confortable : tout est dans les règles.
- Palier de 964 mm de profondeur : le reste de la division des girons s'y ajoute. Longueur côté départ de 2 504 mm pour le palier le plus court.
- Trémie à prévoir pour 2 000 mm d'échappée : 2 130 mm côté départ, sur tout le côté arrivée (2 745 mm).
- Garde-corps : main courante de 900 à 910 mm au-dessus des nez, 25 balustres, écart libre de 105 mm au plus.

Rouvrir cet escalier
sur quart-de-tour.fr

PLAN

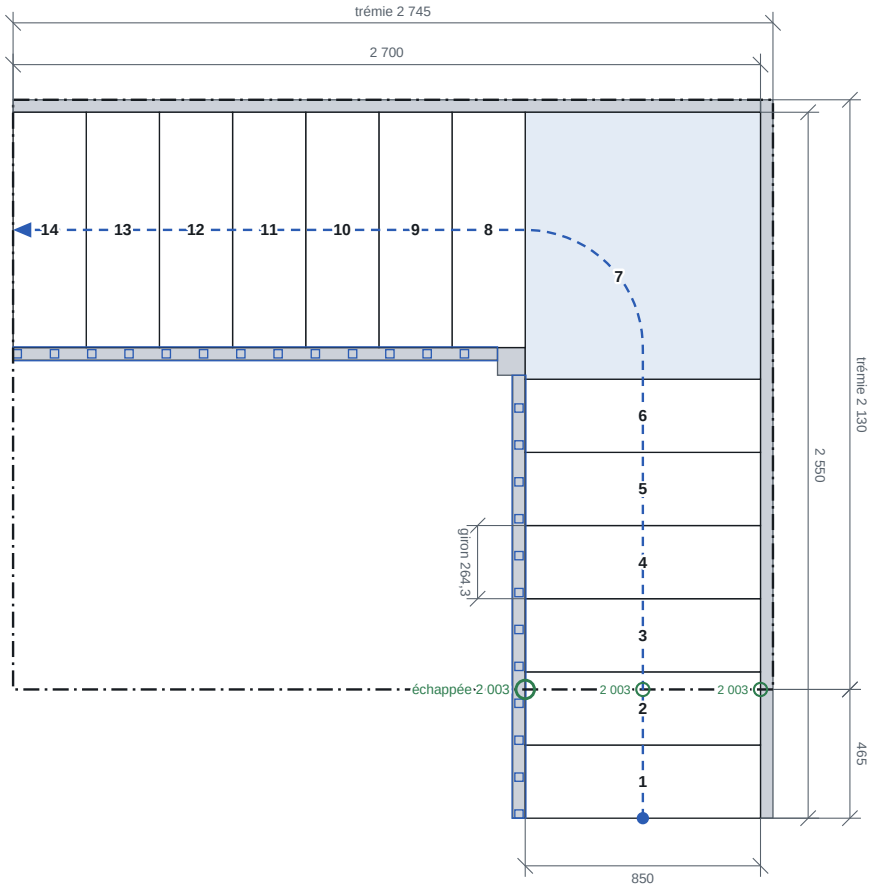

Bois et fiche des marches


BOIS

Essence	**Chêne**
Épaisseur de marche	**40 mm**
Débord de nez	**30 mm**
Profil du nez	**arrondi R10,0 dessus et dessous**
Contremarches	**22 mm, sur la marche**


LIMONS ET ASSEMBLAGE

Épaisseur de limon	**45 mm**
Hauteur du limon de mur	**340 mm**
Hauteur du limon de jour	**330 mm**
Section du poteau	**100 mm**
Encastrement	**15 mm**
Jeu d'assemblage par côté	**0,5 mm**
Garde-corps	**Balustres dans le chant**
Main courante	**50 × 70 mm**

VUE DE CÔTÉ, DÉVELOPPÉE SUR LA LIGNE DE FOULÉE

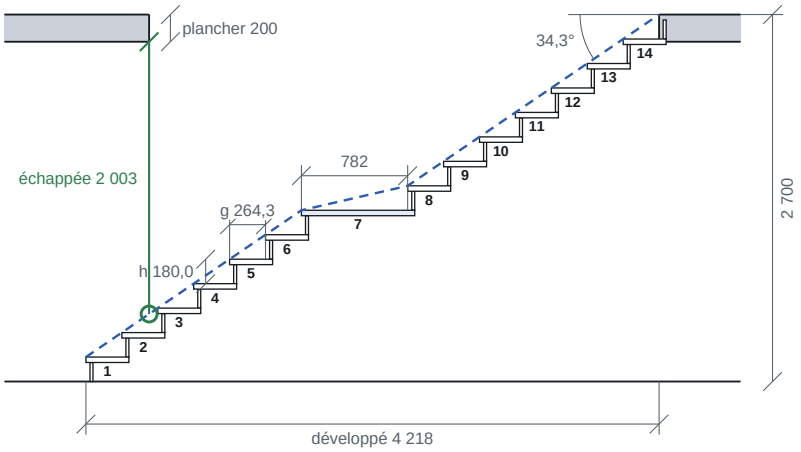

COUPE AU NEZ

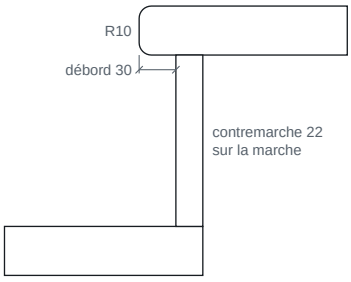

FICHE DES MARCHES

MARCHE	DESSUS	GIRON JOUR	GIRON FOULÉE	GIRON EXTÉRIEUR	LONGUEUR DE NEZ
1	180,0	264,3	264,3	264,3	850,0
2	360,0	264,3	264,3	264,3	850,0
3	540,0	264,3	264,3	264,3	850,0
4	720,0	264,3	264,3	264,3	850,0
5	900,0	264,3	264,3	264,3	850,0
6	1 080,0	264,3	264,3	264,3	850,0
7 palier	1 260,0	114,3	781,9	1 814,3	850,0
8	1 440,0	264,3	264,3	264,3	850,0
9	1 620,0	264,3	264,3	264,3	850,0
10	1 800,0	264,3	264,3	264,3	850,0
11	1 980,0	264,3	264,3	264,3	850,0
12	2 160,0	264,3	264,3	264,3	850,0
13	2 340,0	264,3	264,3	264,3	850,0
14	2 520,0	264,3	264,3	264,3	850,0
Palier	2 700,0				

marches balancées · cotes en millimètres

Girons mesurés de nez à nez. Repères de confort usuels (Blondel 600 à 640 mm, hauteur 160 à 185 mm, giron d'au moins 240 mm, échappée d'au moins 2 000 mm et jamais sous 1 900 mm) : à confronter au NF DTU 36.3 et aux exigences du chantier avant fabrication.

Liste de débit

PIÈCE	QTÉ	LONGUEUR	LARGEUR	ÉPAISSEUR
Limon de jour 1/2	1	2 077	281	45
Limon de jour 2/2	1	2 320	273	45
Limon de mur 1/2	1	2 883	850	45
Limon de mur 2/2	1	3 234	611	45
Marches 1, 2, 3, 4, 5, 6, 8, 9, 10, 11, 12, 13, 14	13	880	317	40
Palier	1	917	980	40
Contremarches 1, 2, 3, 4, 5, 6, 7, 8, 9, 10, 11, 12, 13, 14, 15	15	880	140	22
Main courante 1/2	1	1 997	70	50
Main courante 2/2	1	2 185	70	50
Balustre 1	1	816	30	30
Balustre 2	1	815	30	30
Balustre 3	1	814	30	30
Balustre 4	1	813	30	30
Balustres 5, 6	2	812	30	30
Balustre 7	1	811	30	30
Balustre 8	1	810	30	30
Balustre 9	1	809	30	30
Balustre 10	1	808	30	30
Balustres 11, 12	2	807	30	30
Balustres 13, 14, 15, 16, 17, 18, 19, 20, 21, 22, 23, 24, 25	13	806	30	30
Poteau	1	2 470	100	100

Cotes brutes de débit en millimètres, longueur dans le fil.

Volume brut débité : 0,533 m³ de chêne, soit environ 380 kg (710 kg/m³).

FABRICATION


- Tous les logements tiennent dans les limons, avec au moins 20 mm de bois dessous (limon de jour de 330 mm).
- Palier de 917 × 980 mm : plateau collé à chant, fil le long du nez, logé comme une marche.
- Limon de mur 1/2 (2 883 × 850 mm) plus grand que le plateau de 5 000 × 600 mm : à abouter ou à débiter dans un plateau plus grand.
- Limon de mur 2/2 (3 234 × 611 mm) plus grand que le plateau de 5 000 × 600 mm : à abouter ou à débiter dans un plateau plus grand.

Limons

Vus côté marches, couchés dans le sens du plateau · échelle 1:15


Cotes en millimètres : nez depuis le bout gauche du plateau, hauteurs depuis sa rive basse, angles depuis sa rive. Logements défoncés de 15 mm, jeu de 0,5 mm par côté.

Limon de jour 1/2 2 077 × 281 × 45

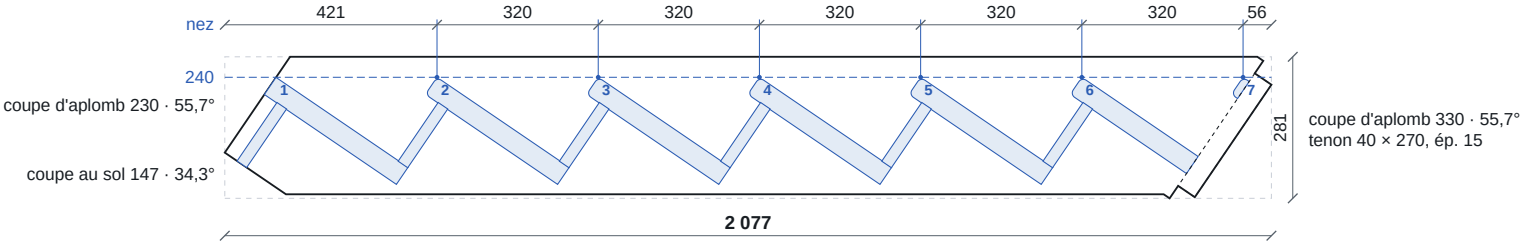

12 mortaises de balustres dans le chant haut.

Limon de jour 2/2 2 320 × 273 × 45

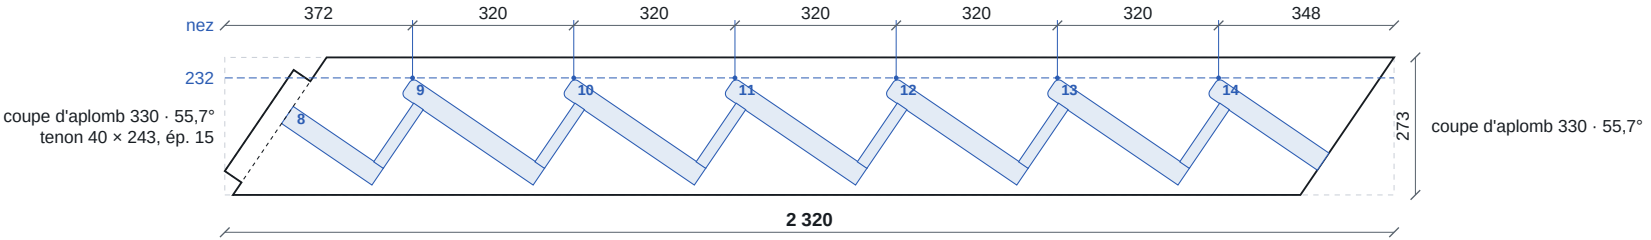


13 mortaises de balustres dans le chant haut.

Limons

Escalier quart-g-a-palier-balustres
Vus côté marches, couchés dans le sens du plateau · échelle 1:15

Cotes en millimètres : nez depuis le bout gauche du plateau, hauteurs depuis sa rive basse, angles depuis sa rive. Logements défoncés de 15 mm, jeu de 0,5 mm par côté.

Limon de mur 1/2 2 883 × 850 × 45

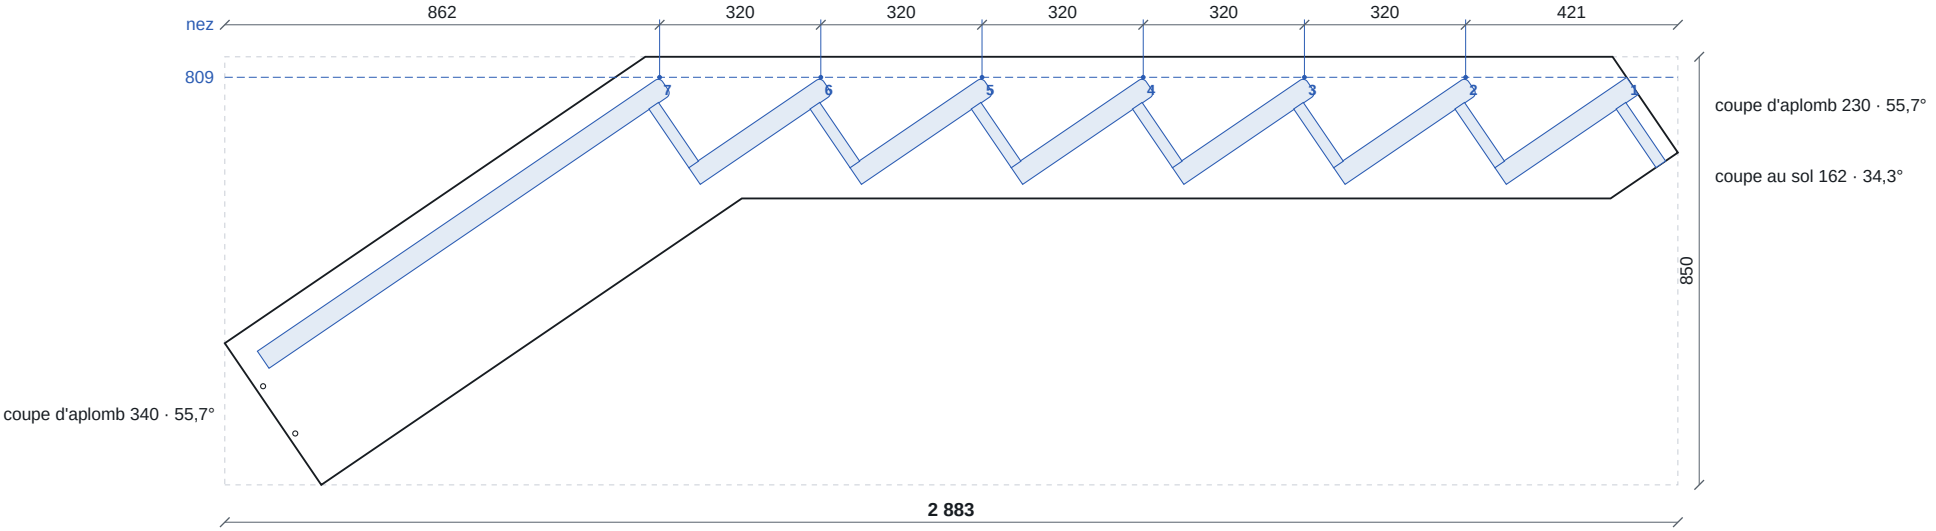

2 perçages Ø 10 traversants pour l'about du limon suivant : x 140, y 102 ; x 76, y 196.

Limon de mur 2/2 3 234 × 611 × 45

