# Escalier dq-d-balustres

Escalier double quart tournant droit · 16 hauteurs de 168,8 mm · giron 282,3 mm

## COTES

| | |
|---|---|
| Hauteur à monter | **2 700 mm** |
| Longueur côté départ | **2 000 mm** |
| Longueur côté fond | **2 400 mm** |
| Longueur côté arrivée | **1 900 mm** |
| Emmarchement | **850 mm** |
| Trémie | **1 950 mm × 2 500 mm** |
| Épaisseur du plancher | **200 mm** |
| Ligne de foulée (depuis le jour) | **425 mm** |
| Marches balancées | **6 et 6 · progressivité 60 %** |
| Premier tour | **marches 3 à 8 · 506 mm à 1 350 mm** |
| Second tour | **marches 9 à 14 · 1 519 mm à 2 363 mm** |

## CONTRÔLES


| | | |
|---|---|---|
| Hauteur de marche | **168,8 mm** | **Bon** |
| Giron | **282,3 mm** | **Bon** |
| Blondel 2h + g | **620 mm** | **Bon** |
| Pente | **30,9 °** | **Bon** |
| Échappée jour | **2 271 mm** | **Bon** |
| Échappée foulée | **2 271 mm** | **Bon** |
| Échappée mur | **2 271 mm** | **Bon** |
| Giron mini au jour | **113 mm** | **Bon** |

## REMARQUES

- Escalier confortable : tout est dans les règles.
- Trémie minimale pour 2 000 mm d'échappée : 1 910 mm côté arrivée, avec 2 500 mm côté fond.
- Garde-corps : main courante de 900 à 1 038 mm au-dessus des nez, 18 balustres, écart libre de 110 mm au plus.

**Rouvrir cet escalier**
sur quart-de-tour.fr

## PLAN

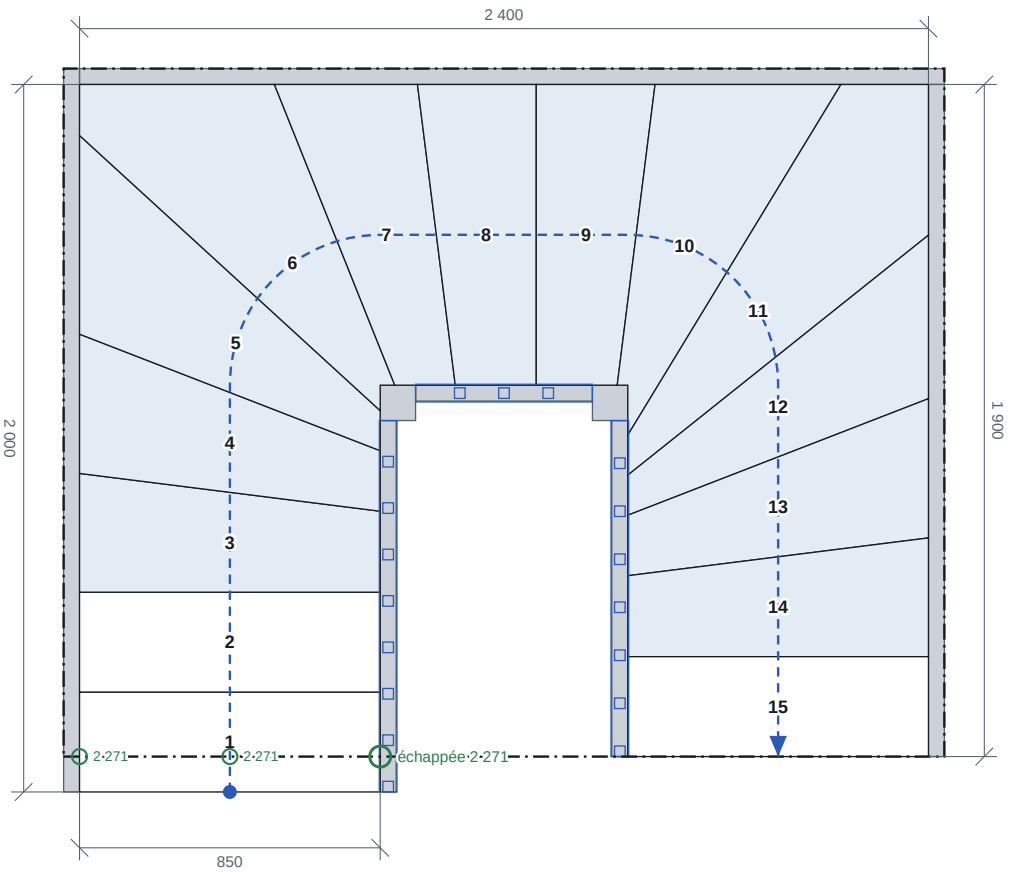

# Bois et fiche des marches

### BOIS

| | |
|---|---|
| Essence | **Chêne** |
| Épaisseur de marche | **40 mm** |
| Débord de nez | **30 mm** |
| Rayon du nez | **10,0 mm** |
| Contremarches | **22 mm** |

### LIMONS ET ASSEMBLAGE

| | |
|---|---|
| Épaisseur de limon | **45 mm** |
| Hauteur du limon de mur | **340 mm** |
| Hauteur du limon de jour | **690 mm** |
| Section du poteau | **100 mm** |
| Encastrement | **15 mm** |
| Jeu d'assemblage par côté | **0,5 mm** |
| Garde-corps | **Balustres dans le chant** |
| Main courante | **50 × 70 mm** |

### FICHE DES MARCHES

| MARCHE | DESSUS | GIRON JOUR | GIRON FOULÉE | GIRON EXTÉRIEUR | LONGUEUR DE NEZ |
|---|---|---|---|---|---|
| 1 | 168,8 | 282,3 | 282,3 | 282,3 | 850,0 |
| 2 | 337,5 | 282,3 | 282,3 | 282,3 | 850,0 |
| 3 | 506,3 | 228,9 | 282,3 | 335,8 | 850,0 |
| 4 | 675,0 | 171,1 | 282,3 | 393,6 | 856,7 |
| 5 | 843,8 | 113,3 | 282,3 | 561,9 | 911,6 |
| 6 | 1 012,5 | 113,3 | 282,3 | 695,0 | 1 152,3 |
| 7 | 1 181,3 | 171,1 | 282,3 | 404,4 | 915,6 |
| 8 | 1 350,0 | 228,9 | 282,3 | 335,8 | 856,7 |
| 9 | 1 518,8 | 228,9 | 282,3 | 335,9 | 850,0 |
| 10 | 1 687,5 | 171,1 | 282,3 | 525,5 | 856,7 |
| 11 | 1 856,3 | 113,3 | 282,3 | 673,3 | 1 160,0 |
| 12 | 2 025,0 | 113,3 | 282,3 | 462,3 | 1 087,6 |
| 13 | 2 193,8 | 171,1 | 282,3 | 393,6 | 911,6 |
| 14 | 2 362,5 | 228,9 | 282,3 | 335,8 | 856,7 |
| 15 | 2 531,3 | 282,3 | 282,3 | 282,3 | 850,0 |
| Palier | 2 700,0 | | | | |

marches balancées · cotes en millimètres

Girons mesurés de nez à nez. Repères de confort usuels (Blondel 600 à 640 mm, hauteur 160 à 185 mm, giron d'au moins 240 mm, échappée d'au moins 2 000 mm et jamais sous 1 900 mm) : à confronter au NF DTU 36.3 et aux exigences du chantier avant fabrication.

# Liste de débit

| PIÈCE | QTÉ | LONGUEUR | LARGEUR | ÉPAISSEUR |
|---|---|---|---|---|
| Limon de jour 1/3 | 1 | 1 466 | 642 | 45 |
| Limon de jour 2/3 | 1 | 1 077 | 578 | 45 |
| Limon de jour 3/3 | 1 | 1 790 | 610 | 45 |
| Limon de mur 1/3 | 1 | 2 312 | 422 | 45 |
| Limon de mur 2/3 | 1 | 2 723 | 452 | 45 |
| Limon de mur 3/3 | 1 | 2 189 | 410 | 45 |
| Marches 1, 2, 15 | 3 | 880 | 335 | 40 |
| Marche 3 | 1 | 880 | 391 | 40 |
| Marche 4 | 1 | 944 | 450 | 40 |
| Marche 5 | 1 | 1 176 | 598 | 40 |
| Marche 6 | 1 | 1 309 | 524 | 40 |
| Marche 7 | 1 | 1 030 | 428 | 40 |
| Marches 8, 14 | 2 | 922 | 387 | 40 |
| Marche 9 | 1 | 1 163 | 391 | 40 |
| Marche 10 | 1 | 1 208 | 589 | 40 |
| Marche 11 | 1 | 1 481 | 474 | 40 |
| Marche 12 | 1 | 1 228 | 410 | 40 |
| Marche 13 | 1 | 1 024 | 420 | 40 |
| Contremarches 1, 2, 3, 9, 15, 16 | 6 | 880 | 129 | 22 |
| Contremarches 4, 8, 14 | 3 | 890 | 129 | 22 |
| Contremarches 5, 13 | 2 | 953 | 129 | 22 |
| Contremarche 6 | 1 | 1 214 | 129 | 22 |
| Contremarche 7 | 1 | 957 | 129 | 22 |
| Contremarche 10 | 1 | 1 172 | 129 | 22 |
| Contremarche 11 | 1 | 1 324 | 129 | 22 |
| Contremarche 12 | 1 | 1 144 | 129 | 22 |
| Main courante 1/3 | 1 | 1 393 | 70 | 50 |
| Main courante 2/3 | 1 | 729 | 70 | 50 |
| Main courante 3/3 | 1 | 1 379 | 70 | 50 |
| Balustre 1 | 1 | 805 | 30 | 30 |
| Balustre 2 | 1 | 827 | 30 | 30 |
| Balustre 3 | 1 | 849 | 30 | 30 |
| Balustre 4 | 1 | 870 | 30 | 30 |
| Balustre 5 | 1 | 892 | 30 | 30 |
| Balustre 6 | 1 | 899 | 30 | 30 |
| Balustre 7 | 1 | 900 | 30 | 30 |
| Balustre 8 | 1 | 871 | 30 | 30 |
| Balustre 9 | 1 | 802 | 30 | 30 |
| Balustre 10 | 1 | 809 | 30 | 30 |
| Balustre 11 | 1 | 816 | 30 | 30 |
| Balustre 12 | 1 | 889 | 30 | 30 |
| Balustre 13 | 1 | 813 | 30 | 30 |
| Balustre 14 | 1 | 797 | 30 | 30 |
| Balustre 15 | 1 | 812 | 30 | 30 |
| Balustre 16 | 1 | 838 | 30 | 30 |
| Balustre 17 | 1 | 883 | 30 | 30 |
| Balustre 18 | 1 | 928 | 30 | 30 |
| Poteau 1 | 1 | 2 230 | 100 | 100 |
| Poteau 2 | 1 | 2 920 | 100 | 100 |

Cotes brutes de débit en millimètres, longueur dans le fil.

**Volume brut débité : 0,660 m³ de chêne, soit environ 470 kg (710 kg/m³).**


### FABRICATION

- Tous les logements tiennent dans les limons, avec au moins 20 mm de bois dessous (limon de jour de 690 mm).
- Limon de jour 1/3 (1 466 × 642 mm) plus grand que le plateau de 5 000 × 600 mm : à abouter ou à débiter dans un plateau plus grand.
- Limon de jour 3/3 (1 790 × 610 mm) plus grand que le plateau de 5 000 × 600 mm : à abouter ou à débiter dans un plateau plus grand.

# Limons


Cotes en millimètres : nez depuis le bout gauche du plateau, hauteurs depuis sa rive basse, angles depuis sa rive. Logements défoncés de 15 mm, jeu de 0,5 mm par côté.

## Limon de jour 1/3 1 466 × 642 × 45

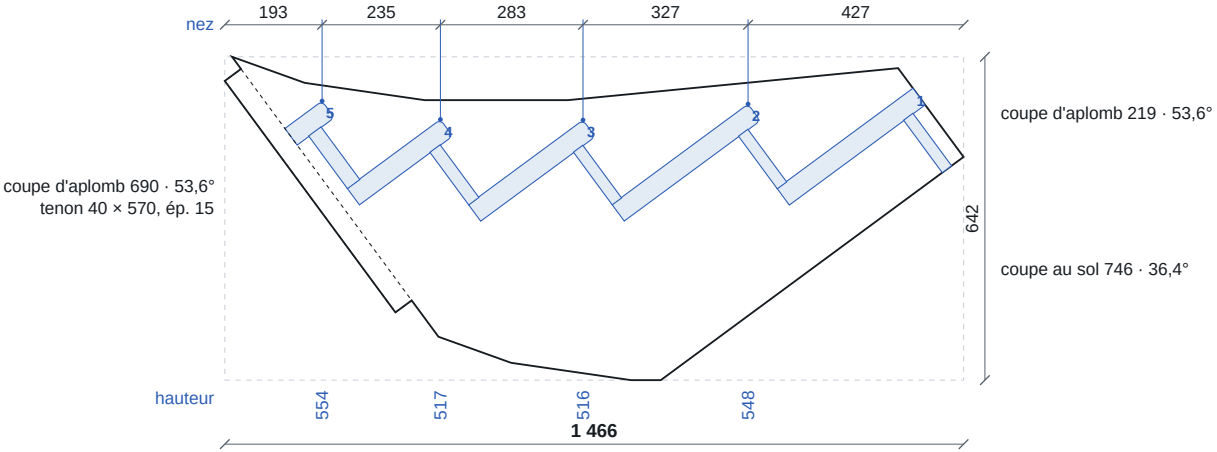


8 mortaises de balustres dans le chant haut.

## Limon de jour 2/3 1 077 × 578 × 45

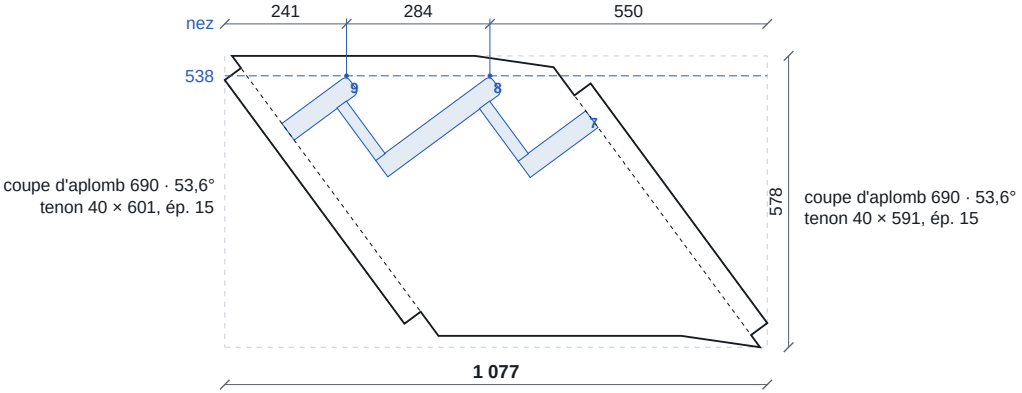



3 mortaises de balustres dans le chant haut.

# Limons


Cotes en millimètres : nez depuis le bout gauche du plateau, hauteurs depuis sa rive basse, angles depuis sa rive. Logements défoncés de 15 mm, jeu de 0,5 mm par côté.

## Limon de jour 3/3 1 790 × 610 × 45

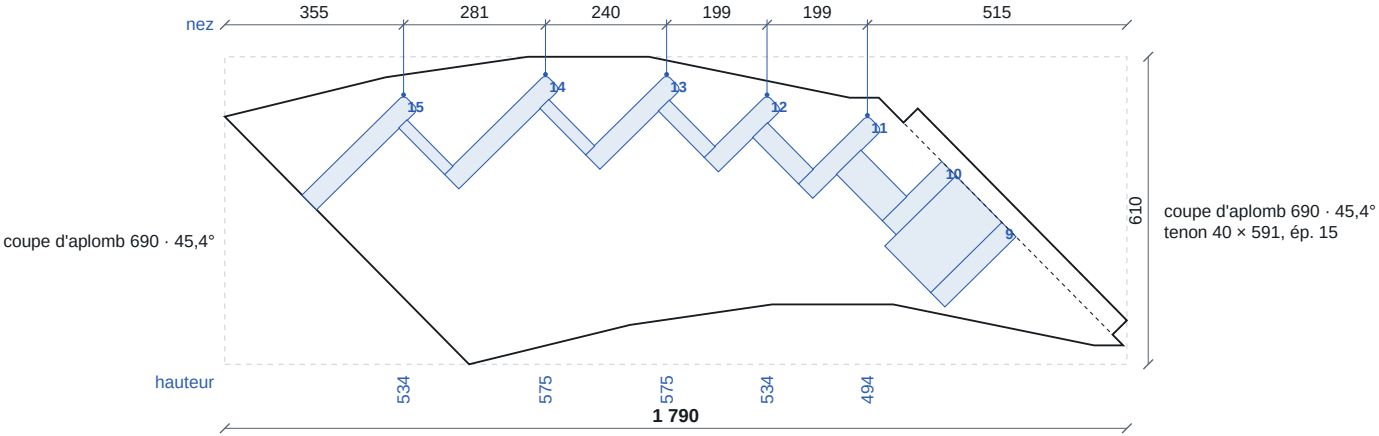


7 mortaises de balustres dans le chant haut.

## Limon de mur 1/3 2 312 × 422 × 45

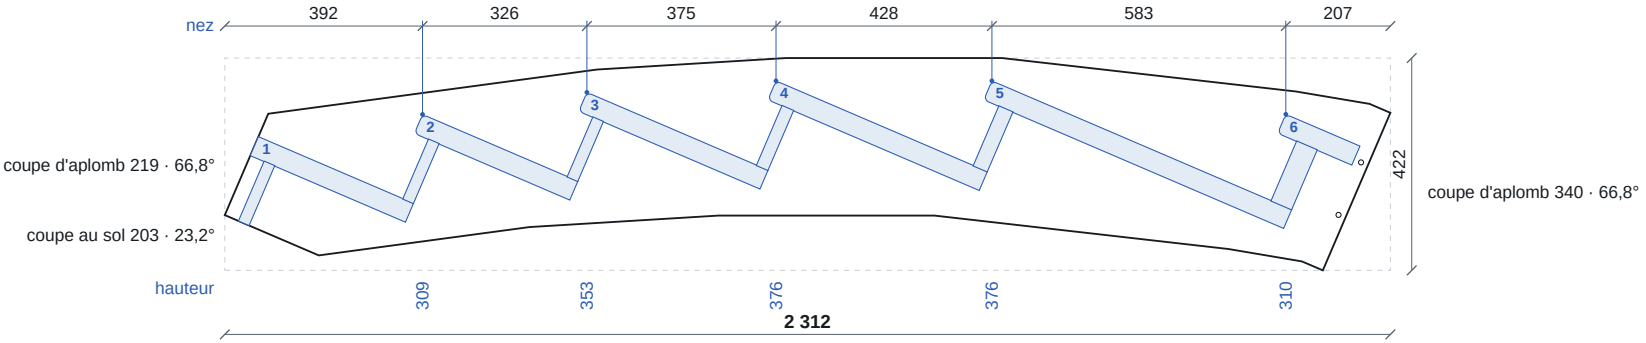



2 perçages Ø 10 traversants pour l'about du limon suivant : x 2 209, y 110 ; x 2 254, y 214.

# Limons

Vus côté marches, couchés dans le sens du plateau · échelle 1:15

Cotes en millimètres : nez depuis le bout gauche du plateau, hauteurs depuis sa rive basse, angles depuis sa rive. Logements défoncés de 15 mm, jeu de 0,5 mm par côté.

## Limon de mur 2/3 2 723 × 452 × 45

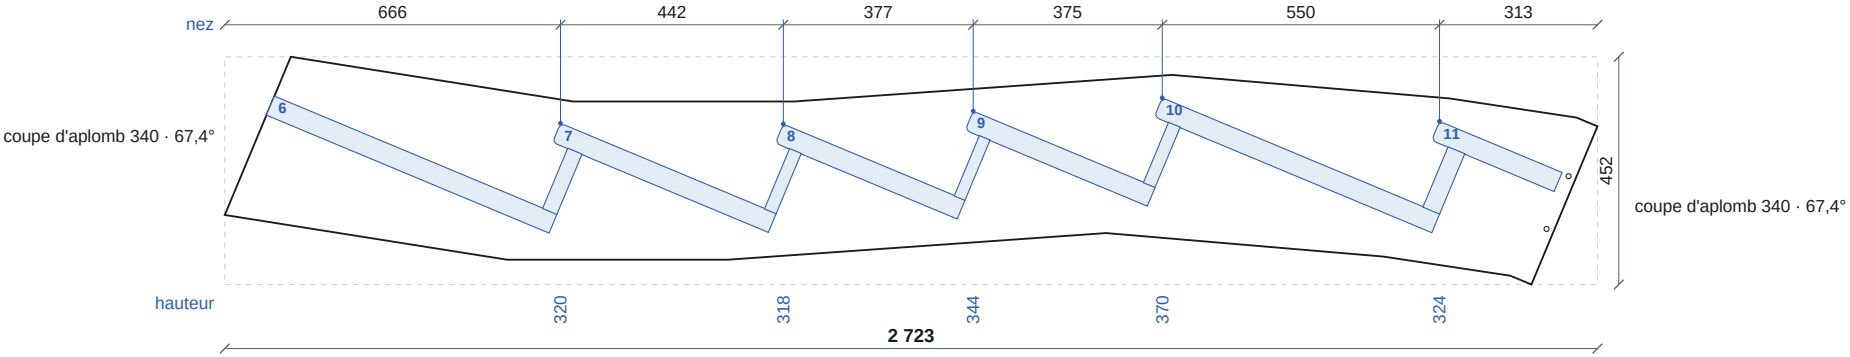


2 perçages Ø 10 traversants pour l'about du limon suivant : x 2 622, y 110 ; x 2 665, y 215.

## Limon de mur 3/3 2 189 × 410 × 45

