Escalier droit-anglaise

Escalier droit · 15 hauteurs de 180,0 mm · giron 260,7 mm

COTES

Hauteur à monter	**2 700 mm**
Reculement	**3 650 mm**
Emmarchement	**850 mm**
Trémie	**3 200 mm**
Épaisseur du plancher	**200 mm**
Ligne de foulée (depuis le jour)	**425 mm**

CONTRÔLES


Hauteur de marche	**180,0 mm**	**Bon**
Giron	**260,7 mm**	**Bon**
Blondel 2h + g	**621 mm**	**Bon**
Pente	**34,6 °**	**Bon**
Échappée	**2 009 mm**	**Bon**
Reculement	**3 650 mm**	

REMARQUES

- Escalier confortable : tout est dans les règles.
- Trémie minimale pour 2 000 mm d'échappée : 3 190 mm de long.
- Garde-corps côté limon droit : main courante de 900 à 900 mm au-dessus des nez, 27 balustres, écart libre de 109 mm au plus.

Rouvrir cet escalier
sur quart-de-tour.fr

PLAN

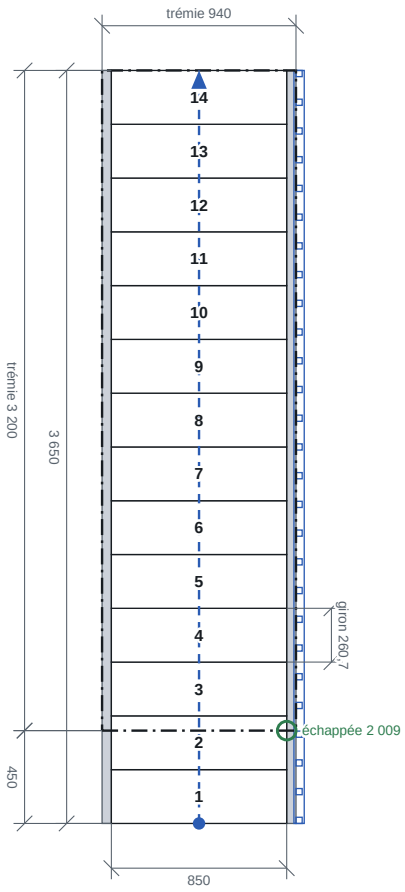

Bois et fiche des marches


BOIS

Essence	**Chêne**
Épaisseur de marche	**40 mm**
Débord de nez	**30 mm**
Rayon du nez	**10,0 mm**
Contremarches	**22 mm**

LIMONS ET ASSEMBLAGE

Épaisseur de limon	**45 mm**
Hauteur de limon	**340 mm**
Encastrement	**15 mm**
Jeu d'assemblage par côté	**0,5 mm**
Garde-corps	**Balustres à l'anglaise**
Main courante	**50 × 70 mm**

VUE DE CÔTÉ, DÉVELOPPÉE SUR LA LIGNE DE FOULÉE

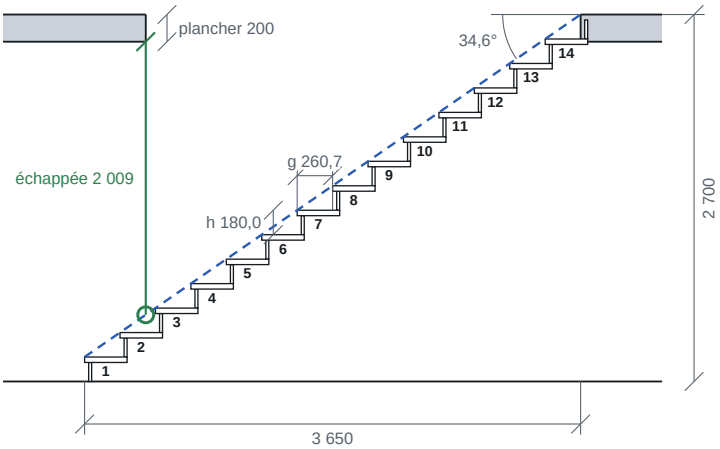

FICHE DES MARCHES

MARCHE	DESSUS	GIRON	LONGUEUR DE NEZ
1	180,0	260,7	850,0
2	360,0	260,7	850,0
3	540,0	260,7	850,0
4	720,0	260,7	850,0
5	900,0	260,7	850,0
6	1 080,0	260,7	850,0
7	1 260,0	260,7	850,0
8	1 440,0	260,7	850,0
9	1 620,0	260,7	850,0
10	1 800,0	260,7	850,0
11	1 980,0	260,7	850,0
12	2 160,0	260,7	850,0
13	2 340,0	260,7	850,0
14	2 520,0	260,7	850,0
Palier	2 700,0		

Cotes en millimètres.

Girons mesurés de nez à nez. Repères de confort usuels (Blondel 600 à 640 mm, hauteur 160 à 185 mm, giron d'au moins 240 mm, échappée d'au moins 2 000 mm et jamais sous 1 900 mm) : à confronter au NF DTU 36.3 et aux exigences du chantier avant fabrication.

Liste de débit

PIÈCE	QTÉ	LONGUEUR	LARGEUR	ÉPAISSEUR
Limon droit	1	4 567	280	45
Limon gauche	1	4 567	280	45
Marches 1, 2, 3, 4, 5, 6, 7, 8, 9, 10, 11, 12, 13, 14	14	880	313	40
Contremarches 1, 2, 3, 4, 5, 6, 7, 8, 9, 10, 11, 12, 13, 14, 15	15	880	140	22
Main courante	1	4 484	70	50
Balustre 1	1	1 026	30	30
Balustre 2	1	1 122	30	30
Balustres 3, 4, 5, 6, 7, 8, 9, 10, 11, 12, 13, 14, 15, 16, 17, 18, 19, 20, 21, 22, 23, 24, 25, 26, 27	25	1 626	30	30

Cotes brutes de débit en millimètres, longueur dans le fil.

Volume brut débité : 0,354 m³ de chêne, soit environ 250 kg (710 kg/m³).

FABRICATION


- Tous les logements tiennent dans les limons, avec au moins 20 mm de bois dessous.
- Toutes les pièces tiennent dans un plateau de 5 000 × 600 mm.

Limons

Escalier droit-anglaise
Vus côté marches, couchés dans le sens du plateau · échelle 1:25


Cotes en millimètres : nez depuis le bout gauche du plateau, hauteurs depuis sa rive basse, angles depuis sa rive. Logements défoncés de 15 mm, jeu de 0,5 mm par côté. Points a, b, c… : voir le traçage à la main.

Limon droit 4 567 × 280 × 45

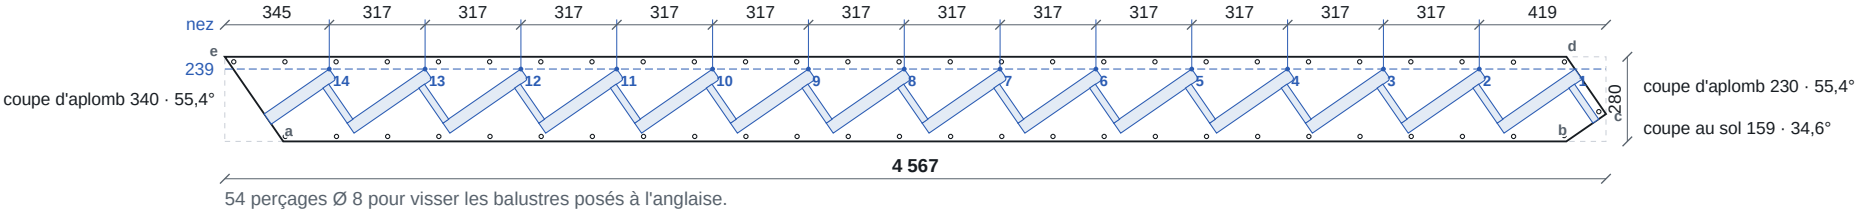

54 perçages Ø 8 pour visser les balustres posés à l'anglaise.

Limon gauche 4 567 × 280 × 45

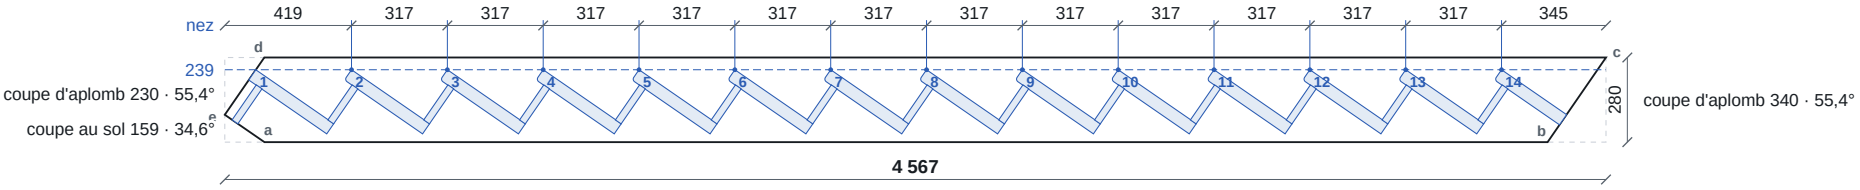

Traçage des limons

1. Dresser la rive basse du plateau et tracer le bout gauche d'équerre : x se mesure le long de la rive depuis ce bout, y d'équerre depuis la rive.
2. Contour : pointer a, b, c… et les joindre dans l'ordre. Les lettres sont aussi sur le dessin des limons.
3. Marches : pointer le nez et le fond, les joindre, c'est le dessus de la marche ; tracer le dessous parallèle, 41 mm plus bas (marche et jeu). Arrondir le bout côté nez au rayon 10.
4. Contremarches : sur le dessus de la marche, depuis le nez, pointer les deux distances données ; tracer d'équerre vers le bas jusqu'au dessus de la marche d'en dessous, ou jusqu'au sol.
5. Défoncer à 15 mm. Tous les dessus de marche d'un limon sont parallèles : la fausse équerre réglée comme indiqué les contrôle.

Limon droit

4 567 × 280 × 45 · dessus de marche à 34,6° sur la rive, montant vers la droite (fausse équerre : 1 000 le long de la rive, 690 d'équerre)

	Nez		Fond		Contremarche, depuis le nez	
Marche	x	y	x	y	de	à
14	345	239	130	91	30	53
13	662	239	404	61	30	53
12	979	239	721	61	30	53
11	1 296	239	1 038	61	30	53
10	1 613	239	1 354	61	30	53
9	1 929	239	1 671	61	30	53
8	2 246	239	1 988	61	30	53
7	2 563	239	2 305	61	30	53
6	2 880	239	2 622	61	30	53
5	3 197	239	2 939	61	30	53
4	3 514	239	3 255	61	30	53
3	3 830	239	3 572	61	30	53
2	4 147	239	3 889	61	30	53
1 *	4 464	239	4 206	61	30	53

Contour		
Point	x	y
a	193	0
b	4 435	0

Point	x	y
c	4 566	91
d	4 435	280

Point	x	y
e	0	280

* logement coupé par l'about : le point « nez » est pris sur l'about.

Limon gauche

4 567 × 280 × 45 · dessus de marche à 34,6° sur la rive, descendant vers la droite (fausse équerre : 1 000 le long de la rive, 690 d'équerre)

	Nez		Fond		Contremarche, depuis le nez	
Marche	x	y	x	y	de	à
1 *	103	239	360	61	30	53
2	419	239	677	61	30	53
3	736	239	994	61	30	53
4	1 053	239	1 311	61	30	53
5	1 369	239	1 628	61	30	53
6	1 686	239	1 944	61	30	53
7	2 003	239	2 261	61	30	53
8	2 320	239	2 578	61	30	53
9	2 637	239	2 895	61	30	53
10	2 953	239	3 212	61	30	53
11	3 270	239	3 528	61	30	53
12	3 587	239	3 845	61	30	53
13	3 904	239	4 162	61	30	53
14	4 221	239	4 436	91	30	53

Contour		
Point	x	y
a	131	0
b	4 373	0

Point	x	y
c	4 566	280
d	131	280

Point	x	y
e	0	91

* logement coupé par l'about : le point « nez » est pris sur l'about.