Escalier dq-d

Escalier double quart tournant droit · 16 hauteurs de 168,8 mm · giron 282,3 mm

COTES

Hauteur à monter	**2 700 mm**
Longueur côté départ	**2 000 mm**
Longueur côté fond	**2 400 mm**
Longueur côté arrivée	**1 900 mm**
Emmarchement	**850 mm**
Trémie	**1 950 mm × 2 500 mm**
Épaisseur du plancher	**200 mm**
Ligne de foulée (depuis le jour)	**425 mm**
Marches balancées	**6 et 6 · progressivité 60 %**
Premier tour	**marches 3 à 8 · 506 mm à 1 350 mm**
Second tour	**marches 9 à 14 · 1 519 mm à 2 363 mm**

CONTRÔLES


Hauteur de marche	**168,8 mm**	**Bon**
Giron	**282,3 mm**	**Bon**
Blondel 2h + g	**620 mm**	**Bon**
Pente	**30,9 °**	**Bon**
Échappée jour	**2 271 mm**	**Bon**
Échappée foulée	**2 271 mm**	**Bon**
Échappée mur	**2 271 mm**	**Bon**
Giron mini au jour	**113 mm**	**Bon**

REMARQUES

- Escalier confortable : tout est dans les règles.
- Giron côté jour de 113 mm : au-dessus des 100 mm, mais beaucoup visent 120 à 150 mm au collet ; 9 marches balancées donnent 120 mm au moins.
- Trémie minimale pour 2 000 mm d'échappée : 1 910 mm côté arrivée, avec 2 500 mm côté fond.
- Pas de garde-corps : côté vide, il en faut un dès 1 m de chute (main courante à 900 mm au moins, NF P01-012). Rien à faire si l'escalier est entre deux murs ou si le garde-corps est posé à part.

Rouvrir cet escalier
sur quart-de-tour.fr

PLAN

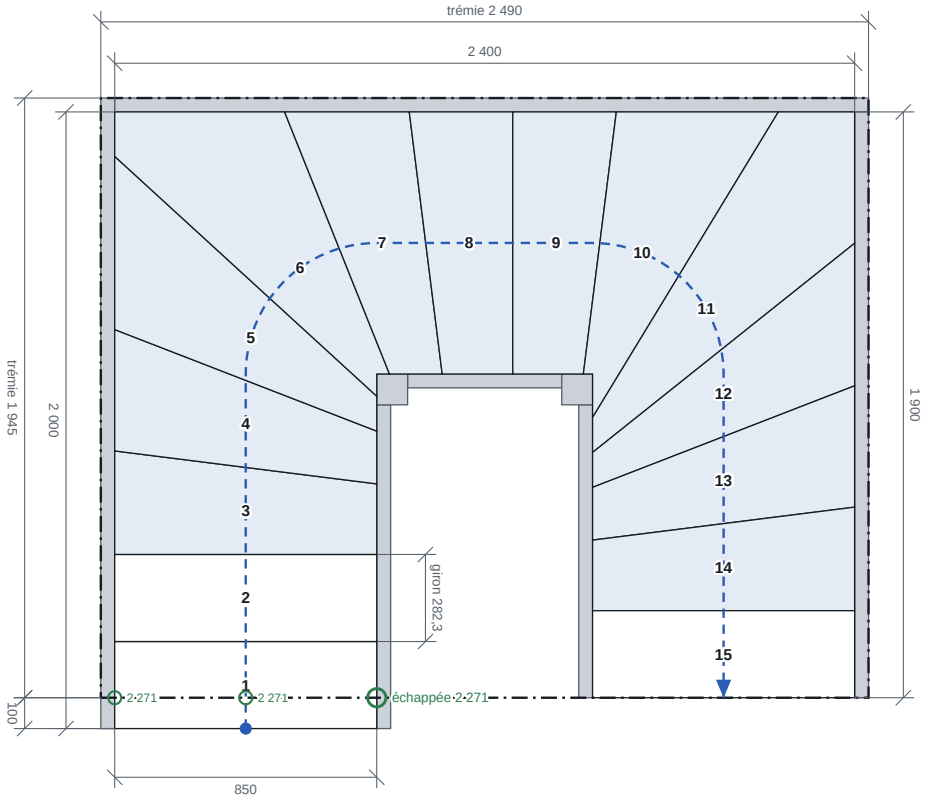

Bois et fiche des marches


BOIS

Essence	**Chêne**
Épaisseur de marche	**40 mm**
Débord de nez	**30 mm**
Rayon du nez	**10,0 mm**
Contremarches	**22 mm**

LIMONS ET ASSEMBLAGE

Épaisseur de limon	**45 mm**
Hauteur du limon de mur	**340 mm**
Hauteur du limon de jour	**690 mm**
Section du poteau	**100 mm**
Encastrement	**15 mm**
Jeu d'assemblage par côté	**0,5 mm**
Garde-corps	**aucun**

VUE DE CÔTÉ, DÉVELOPPÉE SUR LA LIGNE DE FOULÉE

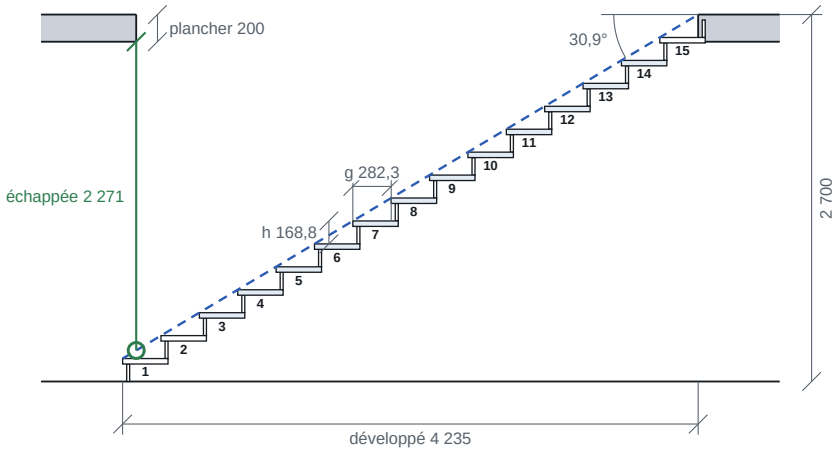

FICHE DES MARCHES

MARCHE	DESSUS	GIRON JOUR	GIRON FOULÉE	GIRON EXTÉRIEUR	LONGUEUR DE NEZ
1	168,8	282,3	282,3	282,3	850,0
2	337,5	282,3	282,3	282,3	850,0
3	506,3	228,9	282,3	335,8	850,0
4	675,0	171,1	282,3	393,6	856,7
5	843,8	113,3	282,3	561,9	911,6
6	1 012,5	113,3	282,3	695,0	1 152,3
7	1 181,3	171,1	282,3	404,4	915,6
8	1 350,0	228,9	282,3	335,8	856,7
9	1 518,8	228,9	282,3	335,9	850,0
10	1 687,5	171,1	282,3	525,5	856,7
11	1 856,3	113,3	282,3	673,3	1 160,0
12	2 025,0	113,3	282,3	462,3	1 087,6
13	2 193,8	171,1	282,3	393,6	911,6
14	2 362,5	228,9	282,3	335,8	856,7
15	2 531,3	282,3	282,3	282,3	850,0
Palier	2 700,0				

marches balancées · cotes en millimètres

Girons mesurés de nez à nez. Repères de confort usuels (Blondel 600 à 640 mm, hauteur 160 à 185 mm, giron d'au moins 240 mm, échappée d'au moins 2 000 mm et jamais sous 1 900 mm) : à confronter au NF DTU 36.3 et aux exigences du chantier avant fabrication.

Liste de débit

PIÈCE	QTÉ	LONGUEUR	LARGEUR	ÉPAISSEUR
Limon de jour 1/3	1	1 466	642	45
Limon de jour 2/3	1	1 077	578	45
Limon de jour 3/3	1	1 790	610	45
Limon de mur 1/3	1	2 312	422	45
Limon de mur 2/3	1	2 723	452	45
Limon de mur 3/3	1	2 189	410	45
Marches 1, 2, 15	3	880	335	40
Marche 3	1	880	391	40
Marche 4	1	944	450	40
Marche 5	1	1 176	598	40
Marche 6	1	1 309	524	40
Marche 7	1	1 030	428	40
Marches 8, 14	2	922	387	40
Marche 9	1	1 163	391	40
Marche 10	1	1 208	589	40
Marche 11	1	1 481	474	40
Marche 12	1	1 228	410	40
Marche 13	1	1 024	420	40
Contremarches 1, 2, 3, 9, 15, 16	6	880	129	22
Contremarches 4, 8, 14	3	890	129	22
Contremarches 5, 13	2	953	129	22
Contremarche 6	1	1 214	129	22
Contremarche 7	1	957	129	22
Contremarche 10	1	1 172	129	22
Contremarche 11	1	1 324	129	22
Contremarche 12	1	1 144	129	22
Poteau 1	1	1 390	100	100
Poteau 2	1	1 970	100	100

Cotes brutes de débit en millimètres, longueur dans le fil.

Volume brut débité : 0,616 m³ de chêne, soit environ 440 kg (710 kg/m³).


FABRICATION

- Tous les logements tiennent dans les limons, avec au moins 20 mm de bois dessous (limon de jour de 690 mm).
- Limon de jour 1/3 (1 466 × 642 mm) plus grand que le plateau de 5 000 × 600 mm : à abouter ou à débiter dans un plateau plus grand.
- Limon de jour 3/3 (1 790 × 610 mm) plus grand que le plateau de 5 000 × 600 mm : à abouter ou à débiter dans un plateau plus grand.


Limons

Cotes en millimètres : nez depuis le bout gauche du plateau, hauteurs depuis sa rive basse, angles depuis sa rive. Logements défoncés de 15 mm, jeu de 0,5 mm par côté.

Limon de jour 1/3 1 466 × 642 × 45

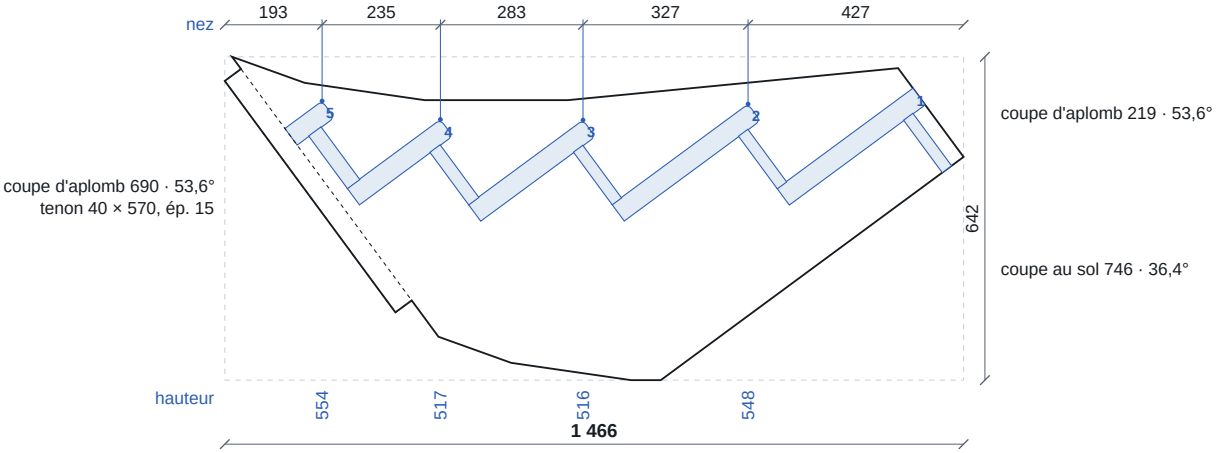


Limon de jour 2/3 1 077 × 578 × 45

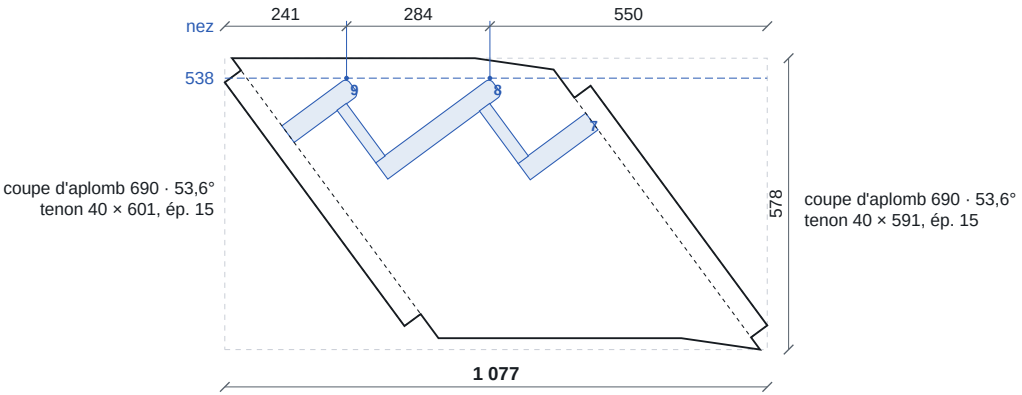


Limons

Cotes en millimètres : nez depuis le bout gauche du plateau, hauteurs depuis sa rive basse, angles depuis sa rive. Logements défoncés de 15 mm, jeu de 0,5 mm par côté.

Limon de jour 3/3 1 790 × 610 × 45

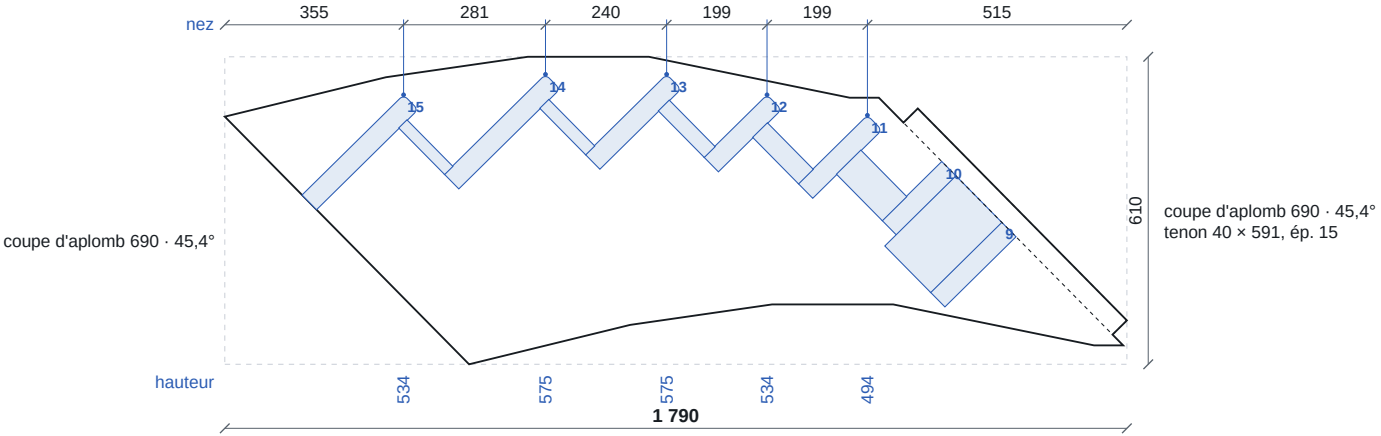

Limon de mur 1/3 2 312 × 422 × 45

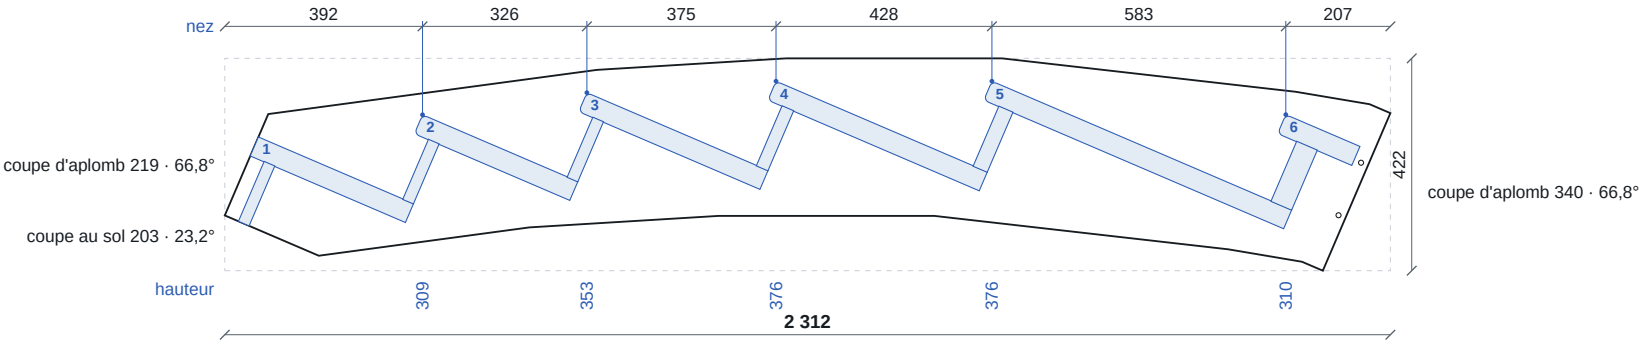


2 perçages Ø 10 traversants pour l'about du limon suivant : x 2 209, y 110 ; x 2 254, y 214.

Limons

Vus côté marches, couchés dans le sens du plateau · échelle 1:15

Cotes en millimètres : nez depuis le bout gauche du plateau, hauteurs depuis sa rive basse, angles depuis sa rive. Logements défoncés de 15 mm, jeu de 0,5 mm par côté.

Limon de mur 2/3 2 723 × 452 × 45

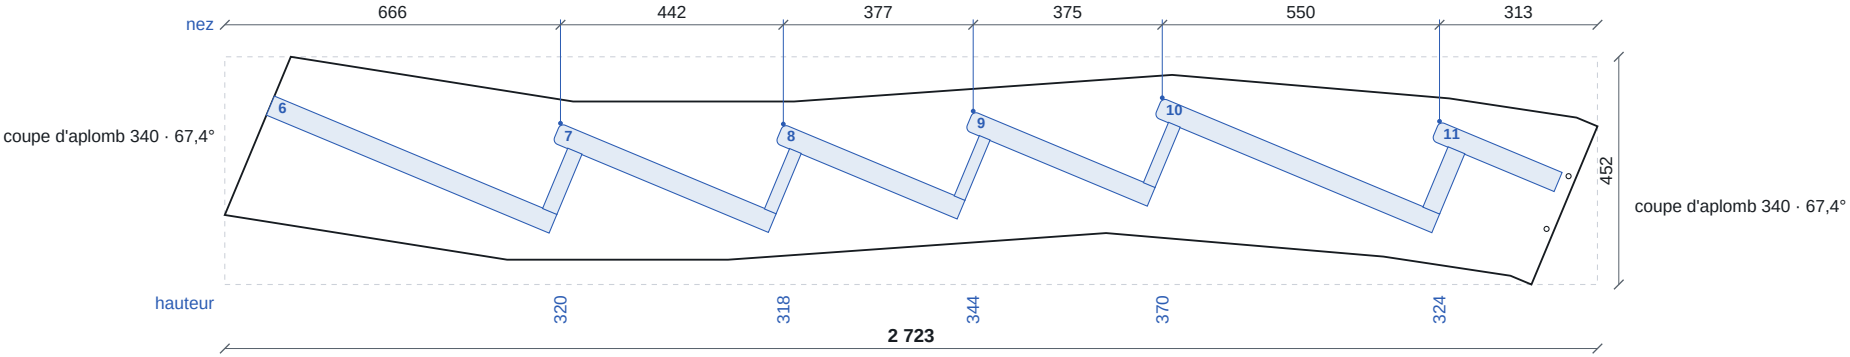

2 perçages Ø 10 traversants pour l'about du limon suivant : x 2 622, y 110 ; x 2 665, y 215.

Limon de mur 3/3 2 189 × 410 × 45

